

Zyra kadastrale komunale / Opštinska katastarska kancelarija: Ferizaj

Zona kadastrale / Katastarska zona: Ferizaj

Lloji i njësisë kadastrale / Vrsta katastarske jedinice : Situacion objektit




Nr. i njësisë kadastrale / Br. katastarske jedinice : 03520-0

Numri i lëndës / Broj predmeta:

Shkalla e zvoglimit / Razmera plana : 1:250

Republika e Kosovës  
Republika Kosova-Republic of Kosova  
Qeveria -Vlada-Government  
Ministria e Mjedisit dhe Planifikimit Hapësinor /Ministarstvo Sredine i Prostornog Planiranja/Ministry of Environment and Spatial Planning  
AGJENCIA KADASTRALE E KOSOVËS/ KATASTARSKA AGENCIJA KOSOVA/ KOSOVA CADASTRAL AGENCY

Pronar: " Kema Residence "

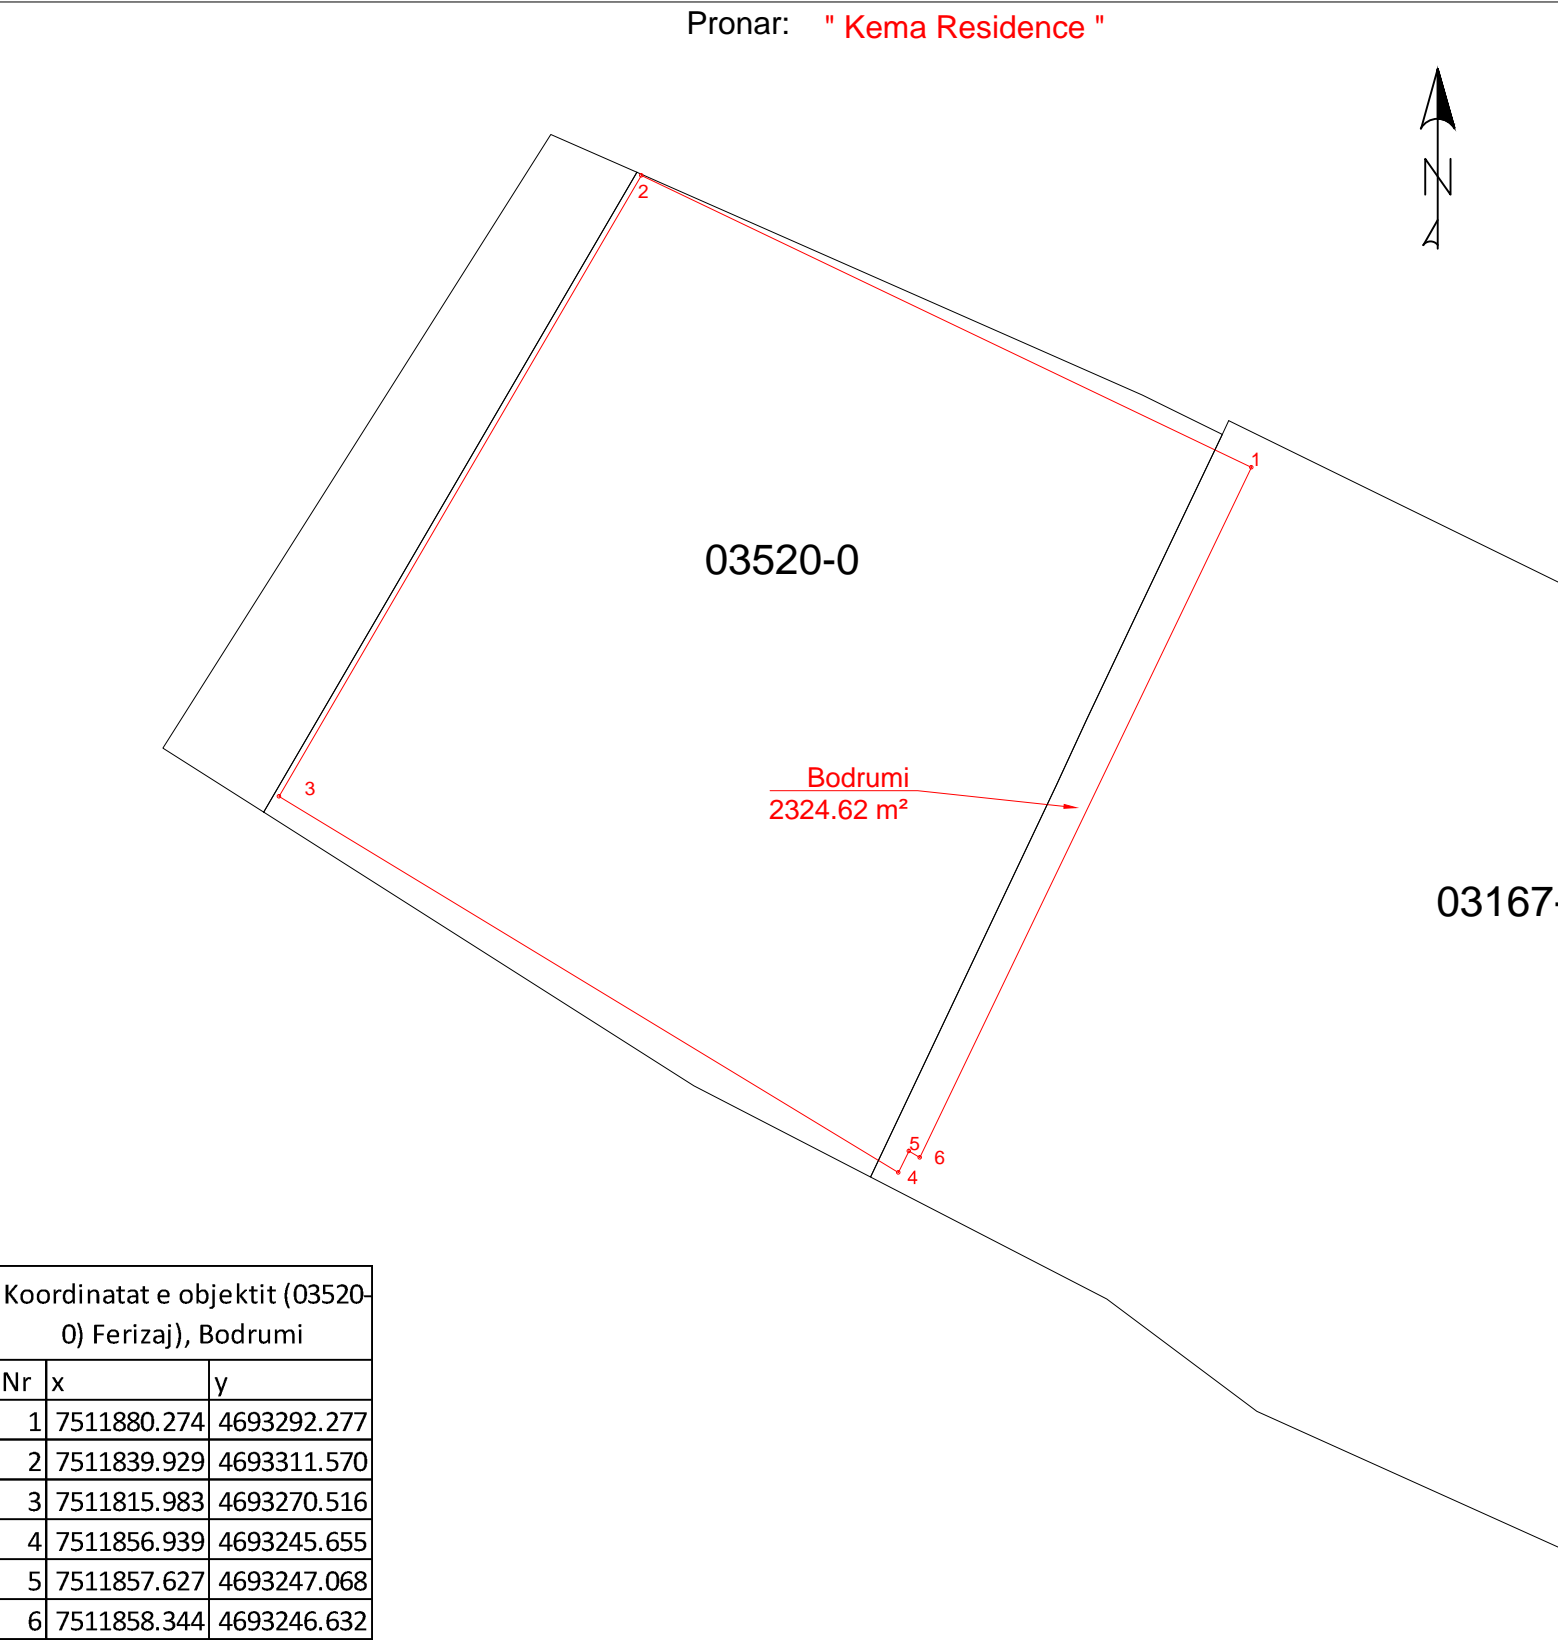

Koordinatat e objektit (03520-0) Ferizaj), Bodrumi		
Nr	x	y
1	7511880.274	4693292.277
2	7511839.929	4693311.570
3	7511815.983	4693270.516
4	7511856.939	4693245.655
5	7511857.627	4693247.068
6	7511858.344	4693246.632

Rilevoi / Snimio: Liridon Sejdiu  
(emri dhe mbiemri i gjeodetit/kompanisë/ ime i prezime geodeta/ kompanije)

Nr. i licencës / Br. licence: 140

Nënshkrimi / Potpis:

Data e rilevimit / Datum snimanja: 18/11/2025

Etazha: Kati -1B

V.V.

Nënshkrimi / Potpis:

Data e aprovimit / Datum usvajanja: