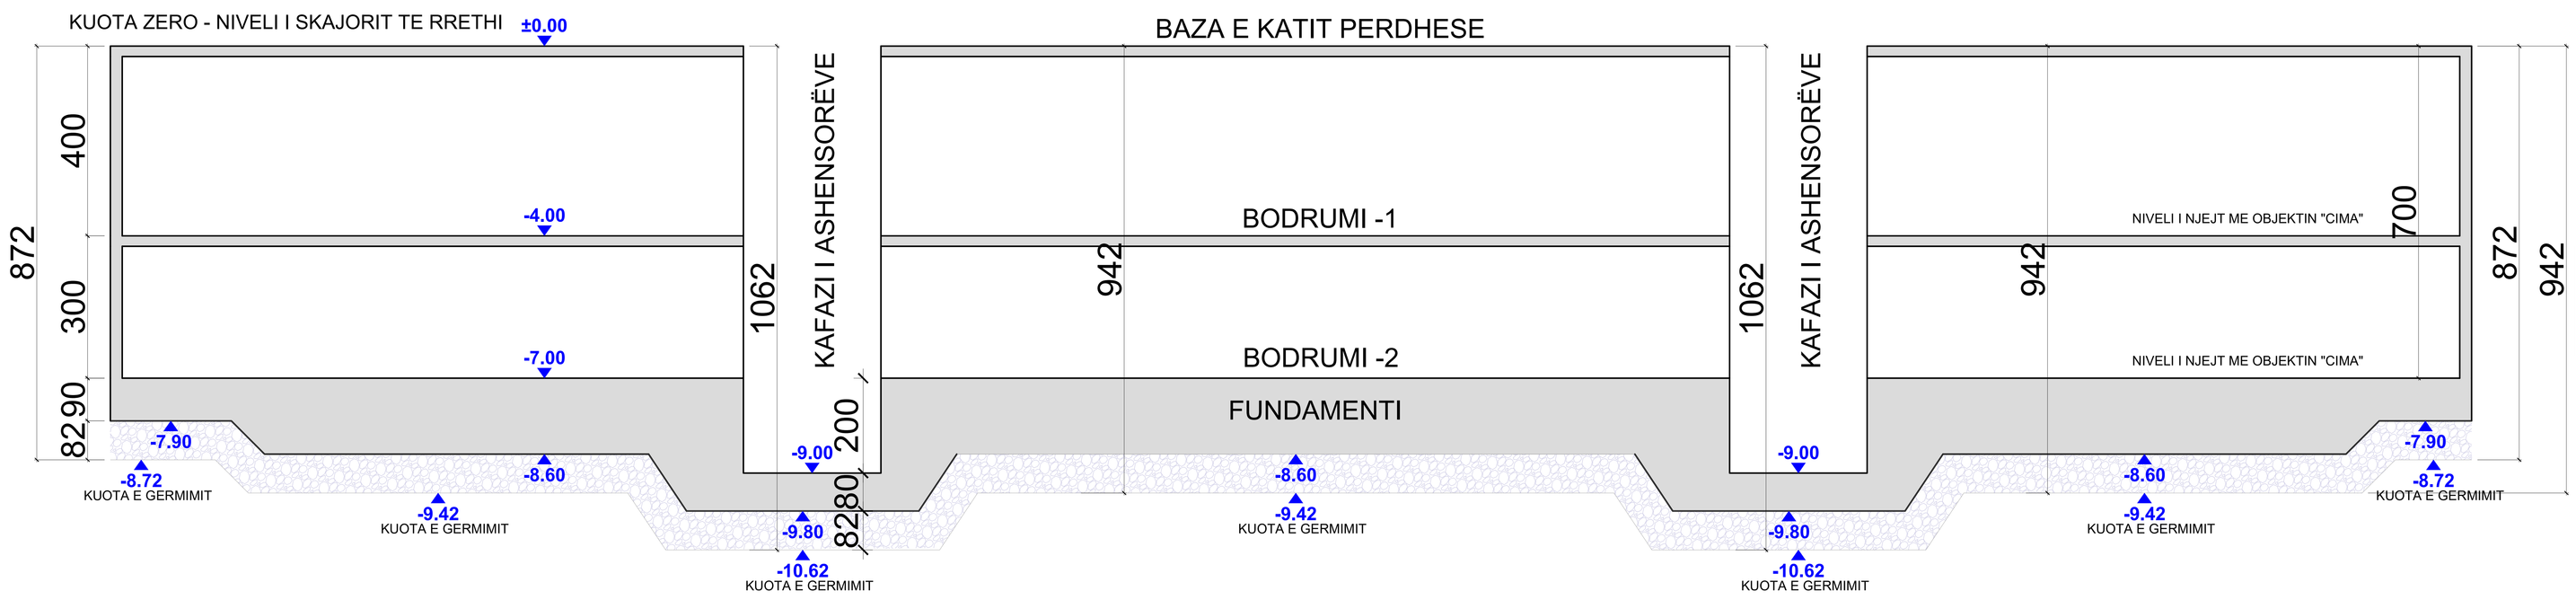

DETALI I SHTREAVE NËN THEMELE

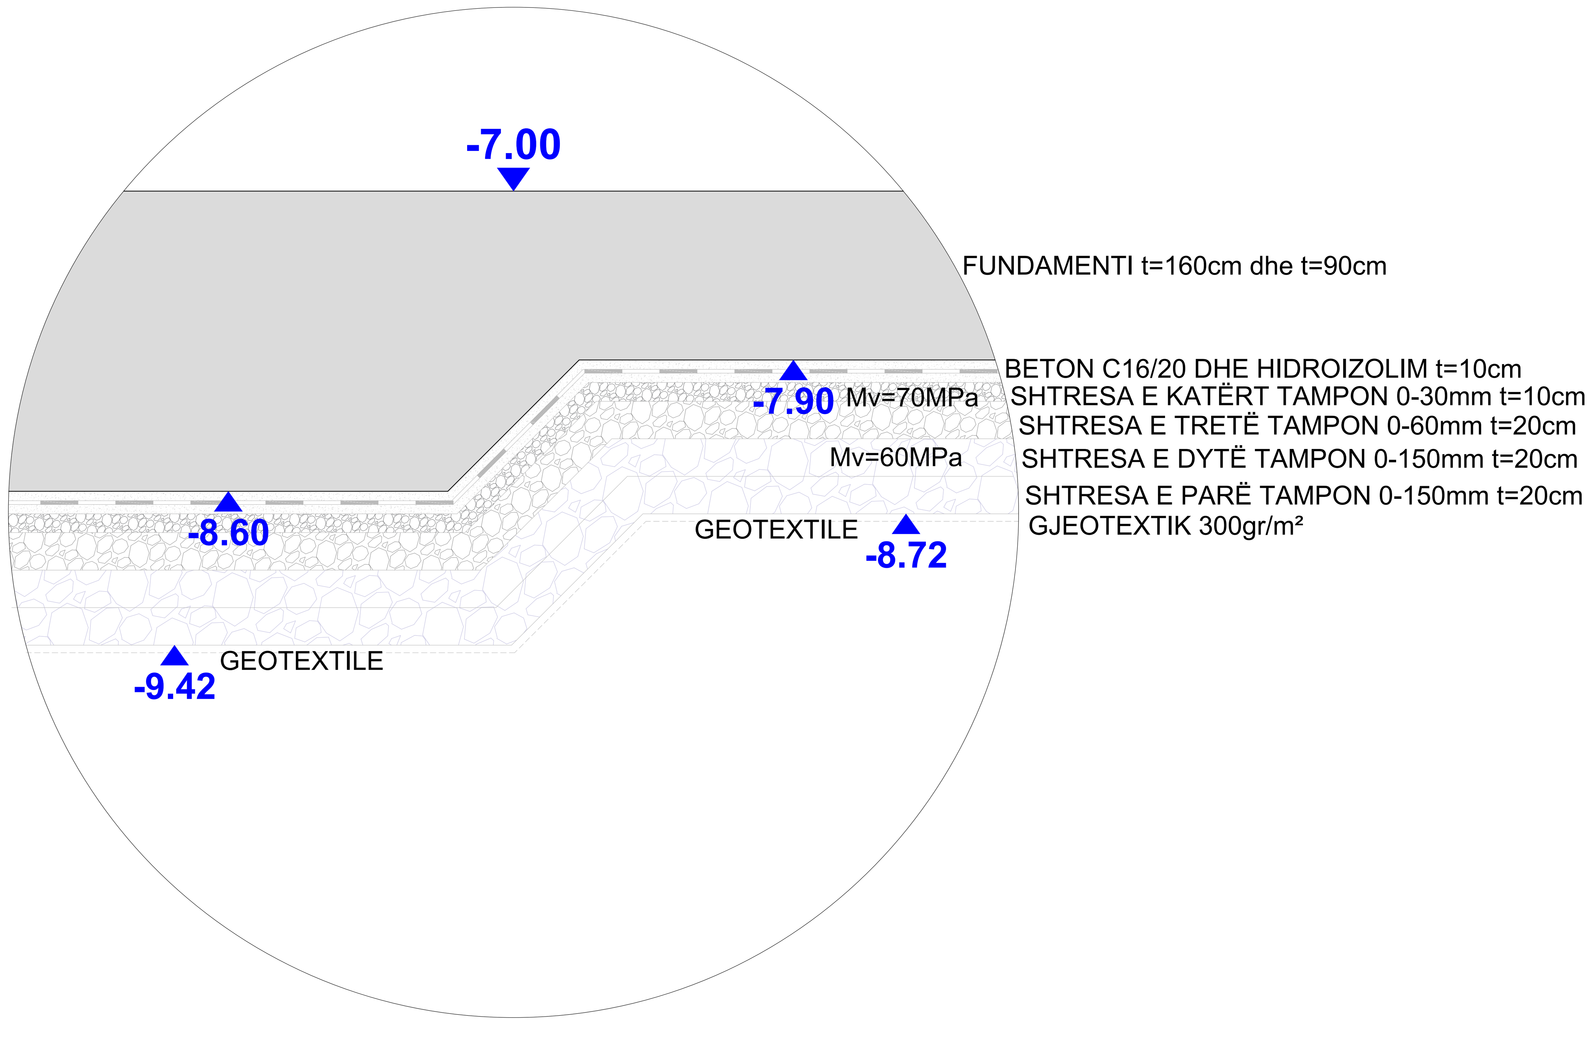

LEGJENDA 01

- SHTYLLA nga themeli deri në kulm
- SHTYLLA nga themeli deri në kuotën zero
- SHTYLLA nga themeli deri në katin e 2të
- MURET BA në bodrum
- MURET BA të berthamës
- MURET bllok sipornëx

LEGJENDA 02

- HAPJET në pllaka dhe mure
- PREREJET
- C01 Pozicionimi i SHTYLLAVE
- M22 Pozicionimi i MUREVE BA
- A Akset

TE DHENAT THEMELORE		
Pos.	EMERTIM	NJËSIA
1	BETON	C 16 / 20
2	ARMATURA	BSt500
3	SHTRESA E PARË	Gravel
4	TRAMBUSA	Gravel
5	NIVELI I SHTRESËS	0-150
6	NIVELI I GJAKUTIT	0-300
7	GJEROSITETI I LEJUESHËM	200 kPa
8	FRATËRI	0,5 FUNDAMENTI DHE KATËRI

Çdo ndryshim i projektimit duhet miratuar me projektuesin dhe ai duhet dokumentuar me shkrim dhe pas miratimit duhet bërë shënim mbi vizatimin ku janë bërë ndryshimet.

Projektuesi nuk mban asnjë përgjegjësi ndaj çdo ndryshimi apo devijimi nga projekti i miratuar.

INVESTITORI: KEMAL BERISHA

OBJEKTI: PËRMBËRTHYES I BANESORE LAMELA (A) - 28+P+15 DHE LAMELA (B) - 28+P+15

LOKACIONI: Fushë Kruja "Peçaku"

STRUKTURA

PLANI GERMIMIT NIVELET DHE SHTRESAT NËN THEMELE PËRJA DHE DETALI

Data/Koha: 10.04.2025

Faza: Projekt Ekzekutiv

Rev. 1 Shtator 2025

STATUSI:Miratuar PROJEKTIMI:Projektim i Miratuar

Format: [L]x[H] = 1190/1334

Shënim: Çdo ndryshim duhet miratuar me projektuesin dhe ai duhet dokumentuar me shkrim dhe pas miratimit duhet bërë shënim mbi vizatimin ku janë bërë ndryshimet.

Projektuesi nuk mban asnjë përgjegjësi ndaj çdo ndryshimi apo devijimi nga projekti i miratuar.

Projektuesi: Arkitekt Vepër Shpk

Adresa: Rruga "Dritan Hoxha" Kodi Postar 1001 Tirana

Llogaritës i Projektit: Inxh. Saad Mahmuti

Nr. Licencës: 0-00-0 PROJEKTIMI I BANESËVE DHE KULLAVE NË KATIN E ÇATISË - SHTRESAT NËN THEMELE - PËRJA DHE DETALI

Emri i Vizatimit: PLANI GERMIMIT NIVELET DHE SHTRESAT NËN THEMELE PËRJA DHE DETALI

Formati: A1

Shënim: Çdo ndryshim duhet miratuar me projektuesin dhe ai duhet dokumentuar me shkrim dhe pas miratimit duhet bërë shënim mbi vizatimin ku janë bërë ndryshimet.

Projektuesi nuk mban asnjë përgjegjësi ndaj çdo ndryshimi apo devijimi nga projekti i miratuar.

Projektuesi: Arkitekt Vepër Shpk

Adresa: Rruga "Dritan Hoxha" Kodi Postar 1001 Tirana

Llogaritës i Projektit: Inxh. Saad Mahmuti

Nr. Licencës: 0-00-0 PROJEKTIMI I BANESËVE DHE KULLAVE NË KATIN E ÇATISË - SHTRESAT NËN THEMELE - PËRJA DHE DETALI

Emri i Vizatimit: PLANI GERMIMIT NIVELET DHE SHTRESAT NËN THEMELE PËRJA DHE DETALI

Formati: A1

S-00.1