Zyra kadastrale komunale / Opštinska katastarska kancelarija: Ferizaj

Zona kadastrale / Katastarska zona: Ferizaj

Lloji i njësisë kadastrale / Vrsta katastarske jedinice : Situacion objektit

Nr. i njësisë kadastrale / Br. katastarske jedinice : 03520-0

Numri i lëndës / Broj predmeta:

Shkalla e zvoglimit / Razmera plana : 1:300

Republika e Kosovës

Republika Kosova-Republic of Kosova

Qeveria -Vlada-Government

Ministria e Mjedisit dhe Planifikimit Hapësinor /Ministarstvo Sredine i Prostornog Planiranja/Ministry of Environment and Spatial Planning


AGJENCIA KADASTRALE E KOSOVËS/ KATASTARSKA AGECIJA KOSOVA/ KOSOVA CADASTRAL AGENCY

Koordinatat e Kati 10 të projektuar

Nr	Y	X	H	Kodi	Përshkrimi	Burimi
1	7511858.648	4693296.964	0.000	Kati 10	Shtëpi-Ndërtesë	PP
2	7511857.746	4693297.395	0.000	Kati 10	Shtëpi-Ndërtesë	PP
3	7511858.026	4693297.982	0.000	Kati 10	Shtëpi-Ndërtesë	PP
4	7511857.034	4693298.456	0.000	Kati 10	Shtëpi-Ndërtesë	PP
5	7511857.315	4693299.042	0.000	Kati 10	Shtëpi-Ndërtesë	PP
6	7511851.676	4693301.739	0.000	Kati 10	Shtëpi-Ndërtesë	PP
7	7511851.396	4693301.152	0.000	Kati 10	Shtëpi-Ndërtesë	PP
8	7511844.810	4693304.302	0.000	Kati 10	Shtëpi-Ndërtesë	PP
9	7511845.090	4693304.888	0.000	Kati 10	Shtëpi-Ndërtesë	PP
10	7511839.452	4693307.584	0.000	Kati 10	Shtëpi-Ndërtesë	PP
11	7511839.171	4693306.998	0.000	Kati 10	Shtëpi-Ndërtesë	PP
12	7511838.179	4693307.472	0.000	Kati 10	Shtëpi-Ndërtesë	PP
13	7511837.899	4693306.886	0.000	Kati 10	Shtëpi-Ndërtesë	PP
14	7511836.996	4693307.317	0.000	Kati 10	Shtëpi-Ndërtesë	PP
15	7511835.810	4693304.836	0.000	Kati 10	Shtëpi-Ndërtesë	PP
16	7511836.712	4693304.405	0.000	Kati 10	Shtëpi-Ndërtesë	PP
17	7511831.018	4693292.497	0.000	Kati 10	Shtëpi-Ndërtesë	PP
18	7511830.116	4693292.928	0.000	Kati 10	Shtëpi-Ndërtesë	PP
19	7511828.649	4693289.861	0.000	Kati 10	Shtëpi-Ndërtesë	PP
20	7511829.551	4693289.429	0.000	Kati 10	Shtëpi-Ndërtesë	PP
21	7511829.271	4693288.843	0.000	Kati 10	Shtëpi-Ndërtesë	PP
22	7511849.118	4693279.352	0.000	Kati 10	Shtëpi-Ndërtesë	PP
23	7511849.398	4693279.938	0.000	Kati 10	Shtëpi-Ndërtesë	PP
24	7511850.301	4693279.507	0.000	Kati 10	Shtëpi-Ndërtesë	PP
25	7511851.767	4693282.574	0.000	Kati 10	Shtëpi-Ndërtesë	PP
26	7511850.865	4693283.006	0.000	Kati 10	Shtëpi-Ndërtesë	PP
27	7511856.560	4693294.914	0.000	Kati 10	Shtëpi-Ndërtesë	PP
28	7511857.462	4693294.483	0.000	Kati 10	Shtëpi-Ndërtesë	PP
29	7511860.173	4693273.844	0.000	Kati 10	Shtëpi-Ndërtesë	PP
30	7511840.326	4693283.335	0.000	Kati 10	Shtëpi-Ndërtesë	PP
31	7511840.045	4693282.748	0.000	Kati 10	Shtëpi-Ndërtesë	PP
32	7511839.143	4693283.180	0.000	Kati 10	Shtëpi-Ndërtesë	PP
33	7511837.677	4693280.112	0.000	Kati 10	Shtëpi-Ndërtesë	PP
34	7511838.579	4693279.681	0.000	Kati 10	Shtëpi-Ndërtesë	PP
35	7511832.884	4693267.772	0.000	Kati 10	Shtëpi-Ndërtesë	PP
36	7511831.982	4693268.204	0.000	Kati 10	Shtëpi-Ndërtesë	PP
37	7511830.796	4693265.723	0.000	Kati 10	Shtëpi-Ndërtesë	PP
38	7511831.698	4693265.291	0.000	Kati 10	Shtëpi-Ndërtesë	PP
39	7511831.417	4693264.705	0.000	Kati 10	Shtëpi-Ndërtesë	PP
40	7511832.410	4693264.230	0.000	Kati 10	Shtëpi-Ndërtesë	PP
41	7511832.129	4693263.644	0.000	Kati 10	Shtëpi-Ndërtesë	PP
42	7511837.768	4693260.948	0.000	Kati 10	Shtëpi-Ndërtesë	PP
43	7511838.048	4693261.534	0.000	Kati 10	Shtëpi-Ndërtesë	PP
44	7511844.634	4693258.385	0.000	Kati 10	Shtëpi-Ndërtesë	PP
45	7511844.354	4693257.799	0.000	Kati 10	Shtëpi-Ndërtesë	PP
46	7511849.992	4693255.102	0.000	Kati 10	Shtëpi-Ndërtesë	PP
47	7511850.272	4693255.689	0.000	Kati 10	Shtëpi-Ndërtesë	PP
48	7511851.265	4693255.214	0.000	Kati 10	Shtëpi-Ndërtesë	PP
49	7511851.545	4693255.800	0.000	Kati 10	Shtëpi-Ndërtesë	PP
50	7511852.447	4693255.369	0.000	Kati 10	Shtëpi-Ndërtesë	PP
51	7511853.634	4693257.850	0.000	Kati 10	Shtëpi-Ndërtesë	PP
52	7511852.732	4693258.281	0.000	Kati 10	Shtëpi-Ndërtesë	PP
53	7511858.426	4693270.190	0.000	Kati 10	Shtëpi-Ndërtesë	PP
54	7511859.328	4693269.758	0.000	Kati 10	Shtëpi-Ndërtesë	PP
55	7511860.795	4693272.826	0.000	Kati 10	Shtëpi-Ndërtesë	PP
56	7511859.893	4693273.257	0.000	Kati 10	Shtëpi-Ndërtesë	PP

Koordinatat e Katit 10 të ekzekutuar

Nr	Y	X	H	Kodi	Përshkrimi	Burimi
1	7511858.665	4693296.968	662.325	Kati 10	Shtëpi-Ndërtesë	PM
2	7511857.770	4693297.399	662.278	Kati 10	Shtëpi-Ndërtesë	PM
3	7511858.042	4693297.977	662.264	Kati 10	Shtëpi-Ndërtesë	PM
4	7511857.060	4693298.483	662.369	Kati 10	Shtëpi-Ndërtesë	PM
5	7511857.314	4693299.039	662.376	Kati 10	Shtëpi-Ndërtesë	PM
6	7511851.679	4693301.745	662.377	Kati 10	Shtëpi-Ndërtesë	PM
7	7511851.402	4693301.168	662.271	Kati 10	Shtëpi-Ndërtesë	PM
8	7511844.793	4693304.320	662.257	Kati 10	Shtëpi-Ndërtesë	PM
9	7511845.081	4693304.888	662.238	Kati 10	Shtëpi-Ndërtesë	PM
10	7511839.472	4693307.566	662.280	Kati 10	Shtëpi-Ndërtesë	PM
11	7511839.174	4693306.978	662.286	Kati 10	Shtëpi-Ndërtesë	PM
12	7511838.206	4693307.472	662.277	Kati 10	Shtëpi-Ndërtesë	PM
13	7511837.924	4693306.867	662.282	Kati 10	Shtëpi-Ndërtesë	PM
14	7511837.053	4693307.294	662.273	Kati 10	Shtëpi-Ndërtesë	PM
15	7511835.883	4693304.811	662.301	Kati 10	Shtëpi-Ndërtesë	PM
16	7511836.748	4693304.409	662.285	Kati 10	Shtëpi-Ndërtesë	PM
17	7511831.004	4693292.497	662.271	Kati 10	Shtëpi-Ndërtesë	PM
18	7511830.108	4693292.916	662.272	Kati 10	Shtëpi-Ndërtesë	PM
19	7511828.656	4693289.839	662.298	Kati 10	Shtëpi-Ndërtesë	PM
20	7511829.545	4693289.433	662.277	Kati 10	Shtëpi-Ndërtesë	PM
21	7511829.279	4693288.810	662.257	Kati 10	Shtëpi-Ndërtesë	PM
22	7511849.114	4693279.344	662.256	Kati 10	Shtëpi-Ndërtesë	PM
23	7511849.401	4693279.924	662.274	Kati 10	Shtëpi-Ndërtesë	PM
24	7511850.310	4693279.503	662.381	Kati 10	Shtëpi-Ndërtesë	PM
25	7511851.771	4693282.563	662.372	Kati 10	Shtëpi-Ndërtesë	PM
26	7511850.861	4693282.988	662.294	Kati 10	Shtëpi-Ndërtesë	PM
27	7511856.563	4693294.913	662.271	Kati 10	Shtëpi-Ndërtesë	PM
28	7511857.452	4693294.462	662.325	Kati 10	Shtëpi-Ndërtesë	PM
29	7511860.159	4693273.847	662.306	Kati 10	Shtëpi-Ndërtesë	PM
30	7511840.305	4693283.335	662.326	Kati 10	Shtëpi-Ndërtesë	PM
31	7511840.030	4693282.735	662.309	Kati 10	Shtëpi-Ndërtesë	PM
32	7511839.132	4693283.166	662.325	Kati 10	Shtëpi-Ndërtesë	PM
33	7511837.690	4693280.092	662.426	Kati 10	Shtëpi-Ndërtesë	PM
34	7511838.542	4693279.668	662.413	Kati 10	Shtëpi-Ndërtesë	PM
35	7511832.861	4693267.780	662.432	Kati 10	Shtëpi-Ndërtesë	PM
36	7511831.979	4693268.210	662.440	Kati 10	Shtëpi-Ndërtesë	PM
37	7511830.809	4693265.706	662.427	Kati 10	Shtëpi-Ndërtesë	PM
38	7511831.691	4693265.303	662.400	Kati 10	Shtëpi-Ndërtesë	PM
39	7511831.424	4693264.721	662.311	Kati 10	Shtëpi-Ndërtesë	PM
40	7511832.386	4693264.197	662.413	Kati 10	Shtëpi-Ndërtesë	PM
41	7511832.133	4693263.652	662.411	Kati 10	Shtëpi-Ndërtesë	PM
42	7511837.794	4693260.967	662.408	Kati 10	Shtëpi-Ndërtesë	PM
43	7511838.069	4693261.529	662.333	Kati 10	Shtëpi-Ndërtesë	PM
44	7511844.628	4693258.364	662.439	Kati 10	Shtëpi-Ndërtesë	PM
45	7511844.360	4693257.811	662.432	Kati 10	Shtëpi-Ndërtesë	PM
46	7511850.004	4693255.106	662.472	Kati 10	Shtëpi-Ndërtesë	PM
47	7511850.273	4693255.660	662.459	Kati 10	Shtëpi-Ndërtesë	PM
48	7511851.287	4693255.206	662.314	Kati 10	Shtëpi-Ndërtesë	PM
49	7511851.560	4693255.788	662.332	Kati 10	Shtëpi-Ndërtesë	PM
50	7511852.456	4693255.352	662.420	Kati 10	Shtëpi-Ndërtesë	PM
51	7511853.642	4693257.844	662.414	Kati 10	Shtëpi-Ndërtesë	PM
52	7511852.761	4693258.261	662.412	Kati 10	Shtëpi-Ndërtesë	PM
53	7511858.422	4693270.175	662.321	Kati 10	Shtëpi-Ndërtesë	PM
54	7511859.315	4693269.751	662.356	Kati 10	Shtëpi-Ndërtesë	PM
55	7511860.782	4693272.823	662.464	Kati 10	Shtëpi-Ndërtesë	PM
56	7511859.889	4693273.243	662.333	Kati 10	Shtëpi-Ndërtesë	PM

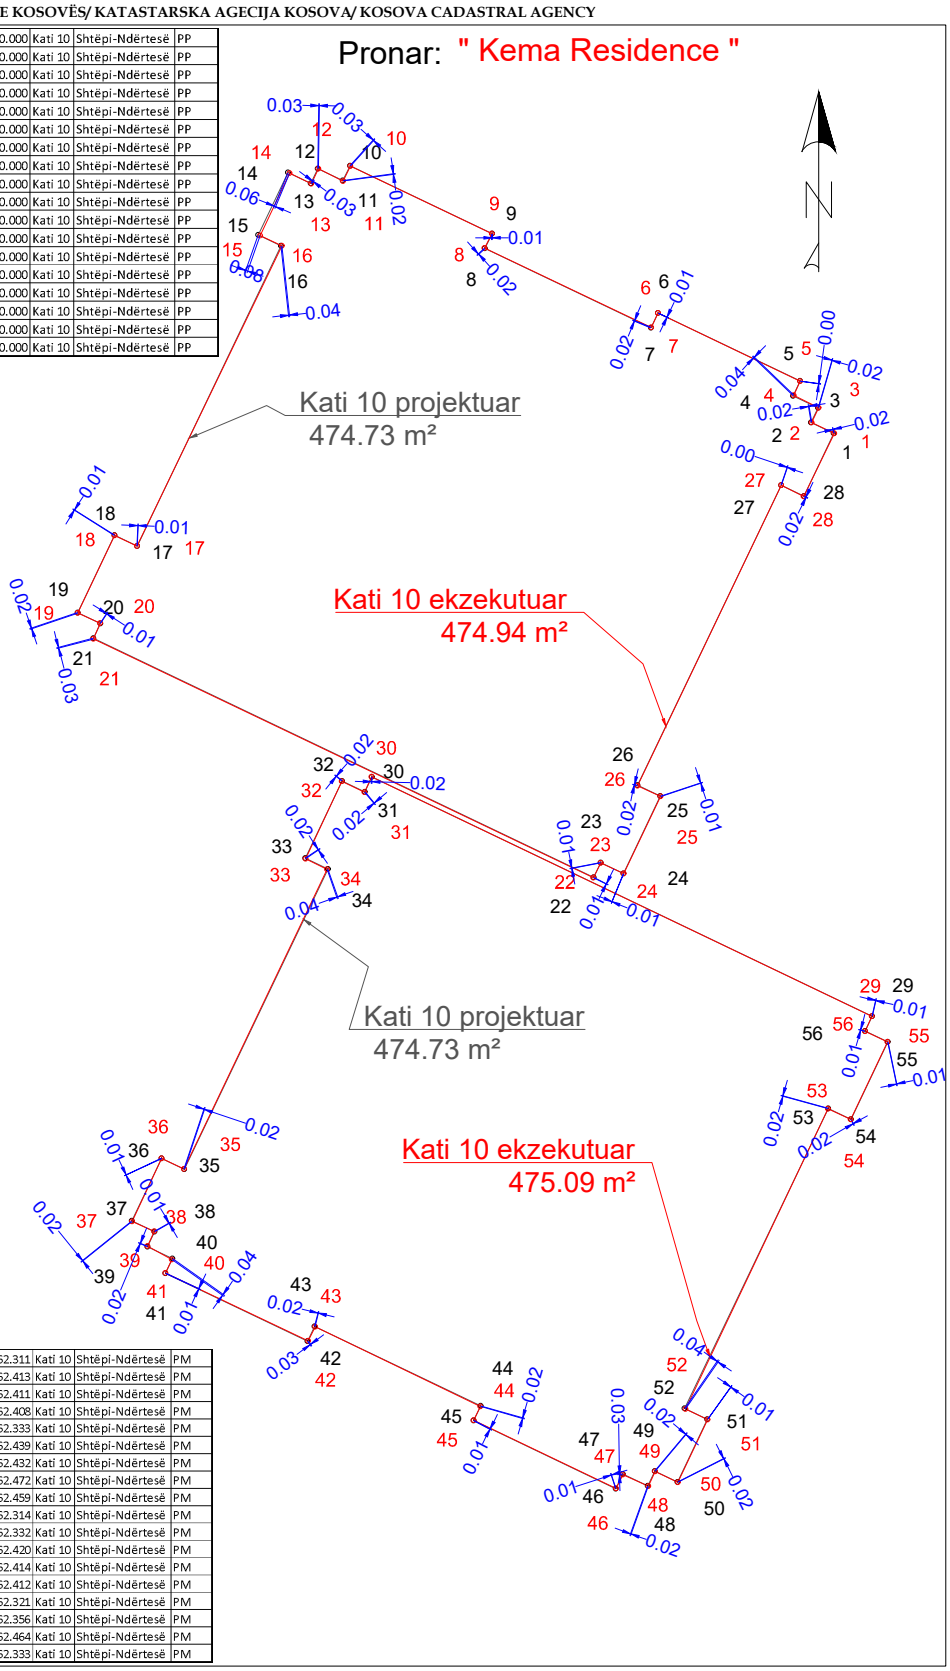

Rilevoi / Snimio: Liridon Sejdiu

(emri dhe mbiemri i gjeodetit/kompanisë/ ime i prezime geodeta/ kompanije)

Etazha: Kati 10

Nr. i licencës / Br. licence: 140

V.V.

Nënshkrimi / Potpis:

Nënshkrimi / Potpis:

Data e rilevimit / Datum snimanja: 10/10/2026

Data e aprovimit / Datum usvajanja: