Zyra kadastrale komunale / Opštinska katastarska kancelarija: Ferizaj

Zona kadastrale / Katastarska zona: Ferizaj

Lloji i njësisë kadastrale / Vrsta katastarske jedinice : Situacion objektit

Nr. i njësisë kadastrale / Br. katastarske jedinice : 03520-0

Numri i lëndës / Broj predmeta:

Shkalla e zvoglimit / Razmera plana : 1:300

Republika e Kosovës

Republika Kosova-Republic of Kosova


Qeveria -Vlada-Government

Ministria e Mjedisit dhe Planifikimit Hapësinor /Ministarstvo Sredine i Prostornog Planiranja/Ministry of Environment and Spatial Planning

AGJENCIA KADASTRALE E KOSOVËS/ KATASTARSKA AGECIJA KOSOVA/ KOSOVA CADASTRAL AGENCY

Koordinatat e Kati 9 të projektuar

Nr	Y	X	H	Kodi	Përshkrimi	Burimi
1	7511858.648	4693296.964	0.000	Kati 9	Shtëpi-Ndërtesë	PP
2	7511857.746	4693297.395	0.000	Kati 9	Shtëpi-Ndërtesë	PP
3	7511858.026	4693297.982	0.000	Kati 9	Shtëpi-Ndërtesë	PP
4	7511857.034	4693298.456	0.000	Kati 9	Shtëpi-Ndërtesë	PP
5	7511857.315	4693299.042	0.000	Kati 9	Shtëpi-Ndërtesë	PP
6	7511851.676	4693301.739	0.000	Kati 9	Shtëpi-Ndërtesë	PP
7	7511851.396	4693301.152	0.000	Kati 9	Shtëpi-Ndërtesë	PP
8	7511844.810	4693304.302	0.000	Kati 9	Shtëpi-Ndërtesë	PP
9	7511845.090	4693304.888	0.000	Kati 9	Shtëpi-Ndërtesë	PP
10	7511839.452	4693307.584	0.000	Kati 9	Shtëpi-Ndërtesë	PP
11	7511839.171	4693306.998	0.000	Kati 9	Shtëpi-Ndërtesë	PP
12	7511838.179	4693307.472	0.000	Kati 9	Shtëpi-Ndërtesë	PP
13	7511837.899	4693306.886	0.000	Kati 9	Shtëpi-Ndërtesë	PP
14	7511836.996	4693307.317	0.000	Kati 9	Shtëpi-Ndërtesë	PP
15	7511835.810	4693304.836	0.000	Kati 9	Shtëpi-Ndërtesë	PP
16	7511836.712	4693304.405	0.000	Kati 9	Shtëpi-Ndërtesë	PP
17	7511831.018	4693292.497	0.000	Kati 9	Shtëpi-Ndërtesë	PP
18	7511830.116	4693292.928	0.000	Kati 9	Shtëpi-Ndërtesë	PP
19	7511828.649	4693289.861	0.000	Kati 9	Shtëpi-Ndërtesë	PP
20	7511829.551	4693289.429	0.000	Kati 9	Shtëpi-Ndërtesë	PP
21	7511829.271	4693288.843	0.000	Kati 9	Shtëpi-Ndërtesë	PP
22	7511849.118	4693279.352	0.000	Kati 9	Shtëpi-Ndërtesë	PP
23	7511849.398	4693279.938	0.000	Kati 9	Shtëpi-Ndërtesë	PP
24	7511850.301	4693279.507	0.000	Kati 9	Shtëpi-Ndërtesë	PP
25	7511851.767	4693282.574	0.000	Kati 9	Shtëpi-Ndërtesë	PP
26	7511850.865	4693283.006	0.000	Kati 9	Shtëpi-Ndërtesë	PP
27	7511856.560	4693294.914	0.000	Kati 9	Shtëpi-Ndërtesë	PP
28	7511857.462	4693294.483	0.000	Kati 9	Shtëpi-Ndërtesë	PP
29	7511860.173	4693273.844	0.000	Kati 9	Shtëpi-Ndërtesë	PP
30	7511840.326	4693283.335	0.000	Kati 9	Shtëpi-Ndërtesë	PP
31	7511840.045	4693282.748	0.000	Kati 9	Shtëpi-Ndërtesë	PP
32	7511839.143	4693283.180	0.000	Kati 9	Shtëpi-Ndërtesë	PP
33	7511837.677	4693280.112	0.000	Kati 9	Shtëpi-Ndërtesë	PP
34	7511838.579	4693279.681	0.000	Kati 9	Shtëpi-Ndërtesë	PP
35	7511832.884	4693267.772	0.000	Kati 9	Shtëpi-Ndërtesë	PP
36	7511831.982	4693268.204	0.000	Kati 9	Shtëpi-Ndërtesë	PP
37	7511830.796	4693265.723	0.000	Kati 9	Shtëpi-Ndërtesë	PP
38	7511831.698	4693265.291	0.000	Kati 9	Shtëpi-Ndërtesë	PP
39	7511831.417	4693264.705	0.000	Kati 9	Shtëpi-Ndërtesë	PP
40	7511832.410	4693264.230	0.000	Kati 9	Shtëpi-Ndërtesë	PP
41	7511832.129	4693263.644	0.000	Kati 9	Shtëpi-Ndërtesë	PP
42	7511837.768	4693260.948	0.000	Kati 9	Shtëpi-Ndërtesë	PP
43	7511838.048	4693261.534	0.000	Kati 9	Shtëpi-Ndërtesë	PP
44	7511844.634	4693258.385	0.000	Kati 9	Shtëpi-Ndërtesë	PP
45	7511844.354	4693257.799	0.000	Kati 9	Shtëpi-Ndërtesë	PP
46	7511849.992	4693255.102	0.000	Kati 9	Shtëpi-Ndërtesë	PP
47	7511850.272	4693255.689	0.000	Kati 9	Shtëpi-Ndërtesë	PP
48	7511851.265	4693255.214	0.000	Kati 9	Shtëpi-Ndërtesë	PP
49	7511851.545	4693255.800	0.000	Kati 9	Shtëpi-Ndërtesë	PP
50	7511852.447	4693255.369	0.000	Kati 9	Shtëpi-Ndërtesë	PP
51	7511853.634	4693257.850	0.000	Kati 9	Shtëpi-Ndërtesë	PP
52	7511852.732	4693258.281	0.000	Kati 9	Shtëpi-Ndërtesë	PP
53	7511858.426	4693270.190	0.000	Kati 9	Shtëpi-Ndërtesë	PP
54	7511859.328	4693269.758	0.000	Kati 9	Shtëpi-Ndërtesë	PP
55	7511860.795	4693272.826	0.000	Kati 9	Shtëpi-Ndërtesë	PP
56	7511859.893	4693273.257	0.000	Kati 9	Shtëpi-Ndërtesë	PP

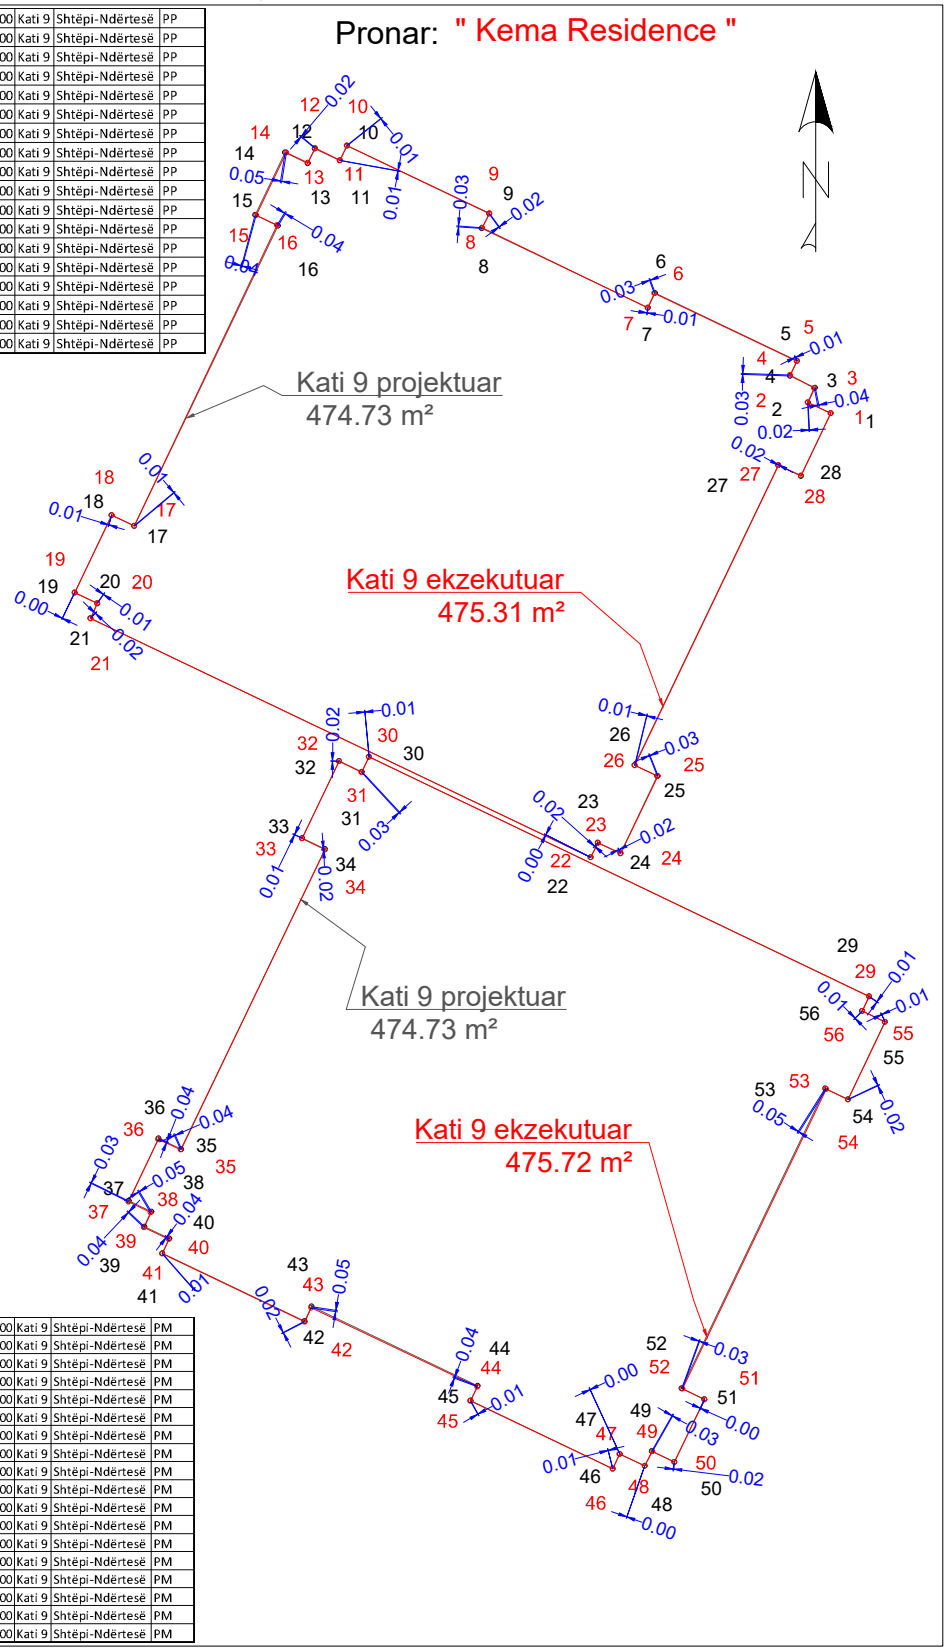

Koordinatat e Katit 9 të ekzekutuar

Nr	Y	X	H	Kodi	Përshkrimi	Burimi
1	7511858.640	4693296.976	659.348	Kati 9	Shtëpi-Ndërtesë	PM
2	7511857.725	4693297.394	659.257	Kati 9	Shtëpi-Ndërtesë	PM
3	7511857.986	4693297.973	659.277	Kati 9	Shtëpi-Ndërtesë	PM
4	7511857.035	4693298.484	659.357	Kati 9	Shtëpi-Ndërtesë	PM
5	7511857.305	4693299.038	659.378	Kati 9	Shtëpi-Ndërtesë	PM
6	7511851.647	4693301.728	659.364	Kati 9	Shtëpi-Ndërtesë	PM
7	7511851.384	4693301.154	659.268	Kati 9	Shtëpi-Ndërtesë	PM
8	7511844.812	4693304.332	659.257	Kati 9	Shtëpi-Ndërtesë	PM
9	7511845.104	4693304.898	659.366	Kati 9	Shtëpi-Ndërtesë	PM
10	7511839.444	4693307.594	659.370	Kati 9	Shtëpi-Ndërtesë	PM
11	7511839.173	4693307.007	659.259	Kati 9	Shtëpi-Ndërtesë	PM
12	7511838.193	4693307.489	659.253	Kati 9	Shtëpi-Ndërtesë	PM
13	7511837.891	4693306.903	659.260	Kati 9	Shtëpi-Ndërtesë	PM
14	7511837.043	4693307.310	659.367	Kati 9	Shtëpi-Ndërtesë	PM
15	7511835.845	4693304.827	659.346	Kati 9	Shtëpi-Ndërtesë	PM
16	7511836.674	4693304.428	659.352	Kati 9	Shtëpi-Ndërtesë	PM
17	7511831.008	4693292.508	659.262	Kati 9	Shtëpi-Ndërtesë	PM
18	7511830.125	4693292.925	659.300	Kati 9	Shtëpi-Ndërtesë	PM
19	7511828.652	4693289.859	659.362	Kati 9	Shtëpi-Ndërtesë	PM
20	7511829.541	4693289.436	659.258	Kati 9	Shtëpi-Ndërtesë	PM
21	7511829.282	4693288.832	659.230	Kati 9	Shtëpi-Ndërtesë	PM
22	7511849.118	4693279.352	659.263	Kati 9	Shtëpi-Ndërtesë	PM
23	7511849.411	4693279.927	659.260	Kati 9	Shtëpi-Ndërtesë	PM
24	7511850.319	4693279.516	659.370	Kati 9	Shtëpi-Ndërtesë	PM
25	7511851.792	4693282.584	659.346	Kati 9	Shtëpi-Ndërtesë	PM
26	7511850.876	4693283.003	659.253	Kati 9	Shtëpi-Ndërtesë	PM
27	7511856.575	4693294.906	659.347	Kati 9	Shtëpi-Ndërtesë	PM
28	7511857.463	4693294.507	659.348	Kati 9	Shtëpi-Ndërtesë	PM
29	7511860.165	4693273.832	659.300	Kati 9	Shtëpi-Ndërtesë	PM
30	7511840.331	4693283.335	659.300	Kati 9	Shtëpi-Ndërtesë	PM
31	7511840.027	4693282.731	659.300	Kati 9	Shtëpi-Ndërtesë	PM
32	7511839.143	4693283.157	659.300	Kati 9	Shtëpi-Ndërtesë	PM
33	7511837.672	4693280.103	659.300	Kati 9	Shtëpi-Ndërtesë	PM
34	7511838.580	4693279.661	659.300	Kati 9	Shtëpi-Ndërtesë	PM
35	7511832.849	4693267.757	659.300	Kati 9	Shtëpi-Ndërtesë	PM
36	7511831.968	4693268.169	659.300	Kati 9	Shtëpi-Ndërtesë	PM
37	7511830.782	4693265.695	659.300	Kati 9	Shtëpi-Ndërtesë	PM
38	7511831.659	4693265.268	659.300	Kati 9	Shtëpi-Ndërtesë	PM
39	7511831.393	4693264.679	659.300	Kati 9	Shtëpi-Ndërtesë	PM
40	7511832.385	4693264.198	659.300	Kati 9	Shtëpi-Ndërtesë	PM
41	7511832.119	4693263.635	659.300	Kati 9	Shtëpi-Ndërtesë	PM
42	7511837.778	4693260.928	659.300	Kati 9	Shtëpi-Ndërtesë	PM
43	7511838.040	4693261.483	659.300	Kati 9	Shtëpi-Ndërtesë	PM
44	7511844.620	4693258.348	659.300	Kati 9	Shtëpi-Ndërtesë	PM
45	7511844.342	4693257.792	659.300	Kati 9	Shtëpi-Ndërtesë	PM
46	7511850.003	4693255.105	659.300	Kati 9	Shtëpi-Ndërtesë	PM
47	7511850.269	4693255.687	659.300	Kati 9	Shtëpi-Ndërtesë	PM
48	7511851.262	4693255.215	659.300	Kati 9	Shtëpi-Ndërtesë	PM
49	7511851.574	4693255.784	659.300	Kati 9	Shtëpi-Ndërtesë	PM
50	7511852.431	4693255.371	659.300	Kati 9	Shtëpi-Ndërtesë	PM
51	7511853.638	4693257.848	659.300	Kati 9	Shtëpi-Ndërtesë	PM
52	7511852.760	4693258.271	659.300	Kati 9	Shtëpi-Ndërtesë	PM
53	7511858.467	4693270.164	659.300	Kati 9	Shtëpi-Ndërtesë	PM
54	7511859.336	4693269.742	659.300	Kati 9	Shtëpi-Ndërtesë	PM
55	7511860.802	4693272.829	659.300	Kati 9	Shtëpi-Ndërtesë	PM
56	7511859.898	4693273.252	659.300	Kati 9	Shtëpi-Ndërtesë	PM

Rilevoi / Snimio: Liridon Sejdiu

(emri dhe mbiemri i gjeodetit/kompanisë/ ime i prezime geodeta/ kompanije)

Etazha: Kati 9

Nr. i licencës / Br. licence: 140

V.V.

Nënshkrimi / Potpis:

Nënshkrimi / Potpis:

Data e rilevimit / Datum snimanja: 23/09/2026

Data e aprovimit / Datum usvajanja: