

Zyra kadastrale komunale / Opštinska katastarska kancelarija: Ferizaj

Zona kadastrale / Katastarska zona: Ferizaj

Lloji i njësisë kadastrale / Vrstë katastarske jedinice : Situacion objektit



Nr. i njësisë kadastrale / Br. katastarske jedinice : 03520-0

Numri i lëndës / Broj predmeta:

Shkalla e zvoglimit / Razmera plana : 1:300


Republika e Kosovës
Republika Kosova-Republic of Kosovo
Qeveria -Vlada-Government

Ministria e Mjedisit dhe Planifikimit Hapësinor /Ministarstvo Sredine i Prostornog Planiranja/Ministry of Environment and Spatial Planning
AGJENCIA KADASTRALE E KOSOVËS/ KATASTARSKA AGENCIJA KOSOVA/ KOSOVA CADASTRAL AGENCY

Koordinatat e Kati 5 të projektuar						
Nr	Y	X	H	Kodi	Përshkrimi	Burimi
1	7511858.648	4693296.964	0.000	Kati 5	Shtëpi-Ndërtesë	PP
2	7511857.746	4693297.395	0.000	Kati 5	Shtëpi-Ndërtesë	PP
3	7511858.026	4693297.982	0.000	Kati 5	Shtëpi-Ndërtesë	PP
4	7511857.034	4693298.456	0.000	Kati 5	Shtëpi-Ndërtesë	PP
5	7511857.315	4693299.042	0.000	Kati 5	Shtëpi-Ndërtesë	PP
6	7511851.676	4693301.739	0.000	Kati 5	Shtëpi-Ndërtesë	PP
7	7511851.396	4693301.152	0.000	Kati 5	Shtëpi-Ndërtesë	PP
8	7511844.810	4693304.302	0.000	Kati 5	Shtëpi-Ndërtesë	PP
9	7511845.090	4693304.888	0.000	Kati 5	Shtëpi-Ndërtesë	PP
10	7511839.452	4693307.584	0.000	Kati 5	Shtëpi-Ndërtesë	PP
11	7511839.171	4693306.998	0.000	Kati 5	Shtëpi-Ndërtesë	PP
12	7511838.179	4693307.472	0.000	Kati 5	Shtëpi-Ndërtesë	PP
13	7511837.899	4693306.886	0.000	Kati 5	Shtëpi-Ndërtesë	PP
14	7511836.996	4693307.317	0.000	Kati 5	Shtëpi-Ndërtesë	PP
15	7511835.810	4693304.836	0.000	Kati 5	Shtëpi-Ndërtesë	PP
16	7511836.712	4693304.405	0.000	Kati 5	Shtëpi-Ndërtesë	PP
17	7511831.018	4693292.497	0.000	Kati 5	Shtëpi-Ndërtesë	PP
18	7511830.116	4693292.928	0.000	Kati 5	Shtëpi-Ndërtesë	PP
19	7511828.649	4693289.861	0.000	Kati 5	Shtëpi-Ndërtesë	PP
20	7511829.551	4693289.429	0.000	Kati 5	Shtëpi-Ndërtesë	PP
21	7511829.271	4693288.843	0.000	Kati 5	Shtëpi-Ndërtesë	PP
22	7511849.118	4693279.352	0.000	Kati 5	Shtëpi-Ndërtesë	PP
23	7511849.398	4693279.938	0.000	Kati 5	Shtëpi-Ndërtesë	PP
24	7511850.301	4693279.507	0.000	Kati 5	Shtëpi-Ndërtesë	PP
25	7511851.767	4693282.574	0.000	Kati 5	Shtëpi-Ndërtesë	PP
26	7511850.865	4693283.006	0.000	Kati 5	Shtëpi-Ndërtesë	PP
27	7511856.560	4693294.914	0.000	Kati 5	Shtëpi-Ndërtesë	PP
28	7511857.462	4693294.483	0.000	Kati 5	Shtëpi-Ndërtesë	PP
29	7511860.173	4693273.844	0.000	Kati 5	Shtëpi-Ndërtesë	PP
30	7511840.326	4693283.335	0.000	Kati 5	Shtëpi-Ndërtesë	PP
31	7511840.045	4693282.748	0.000	Kati 5	Shtëpi-Ndërtesë	PP
32	7511839.143	4693283.180	0.000	Kati 5	Shtëpi-Ndërtesë	PP
33	7511837.677	4693280.112	0.000	Kati 5	Shtëpi-Ndërtesë	PP
34	7511838.579	4693279.681	0.000	Kati 5	Shtëpi-Ndërtesë	PP
35	7511832.884	4693267.772	0.000	Kati 5	Shtëpi-Ndërtesë	PP
36	7511831.982	4693268.204	0.000	Kati 5	Shtëpi-Ndërtesë	PP
37	7511830.796	4693265.723	0.000	Kati 5	Shtëpi-Ndërtesë	PP
38	7511831.698	4693265.291	0.000	Kati 5	Shtëpi-Ndërtesë	PP

Koordinatat e Katit 5 të ekzekutuar						
Nr	Y	X	H	Kodi	Përshkrimi	Burimi
1	7511858.655	4693296.952	647.009	Kati 5	Shtëpi-Ndërtesë	PM
2	7511857.768	4693297.395	647.002	Kati 5	Shtëpi-Ndërtesë	PM
3	7511858.026	4693297.986	646.999	Kati 5	Shtëpi-Ndërtesë	PM
4	7511857.044	4693298.453	647.011	Kati 5	Shtëpi-Ndërtesë	PM
5	7511857.308	4693299.047	647.008	Kati 5	Shtëpi-Ndërtesë	PM
6	7511851.682	4693301.735	646.994	Kati 5	Shtëpi-Ndërtesë	PM
7	7511851.392	4693301.151	646.988	Kati 5	Shtëpi-Ndërtesë	PM
8	7511844.818	4693304.345	647.092	Kati 5	Shtëpi-Ndërtesë	PM
9	7511845.083	4693304.894	646.986	Kati 5	Shtëpi-Ndërtesë	PM
10	7511839.434	4693307.585	646.987	Kati 5	Shtëpi-Ndërtesë	PM
11	7511839.161	4693307.029	647.001	Kati 5	Shtëpi-Ndërtesë	PM
12	7511838.203	4693307.476	643.937	Kati 5	Shtëpi-Ndërtesë	PM
13	7511837.881	4693306.912	647.002	Kati 5	Shtëpi-Ndërtesë	PM
14	7511837.014	4693307.325	647.008	Kati 5	Shtëpi-Ndërtesë	PM
15	7511835.835	4693304.847	647.139	Kati 5	Shtëpi-Ndërtesë	PM
16	7511836.705	4693304.421	646.994	Kati 5	Shtëpi-Ndërtesë	PM
17	7511830.998	4693292.513	646.989	Kati 5	Shtëpi-Ndërtesë	PM
18	7511830.085	4693292.949	647.109	Kati 5	Shtëpi-Ndërtesë	PM
19	7511828.640	4693289.850	647.098	Kati 5	Shtëpi-Ndërtesë	PM
20	7511829.521	4693289.432	647.010	Kati 5	Shtëpi-Ndërtesë	PM
21	7511829.255	4693288.845	647.014	Kati 5	Shtëpi-Ndërtesë	PM
22	7511849.072	4693279.366	647.044	Kati 5	Shtëpi-Ndërtesë	PM
23	7511849.347	4693279.960	647.006	Kati 5	Shtëpi-Ndërtesë	PM
24	7511850.242	4693279.512	647.112	Kati 5	Shtëpi-Ndërtesë	PM
25	7511851.765	4693282.569	647.136	Kati 5	Shtëpi-Ndërtesë	PM
26	7511850.889	4693283.004	647.139	Kati 5	Shtëpi-Ndërtesë	PM
27	7511856.563	4693294.916	646.999	Kati 5	Shtëpi-Ndërtesë	PM
28	7511857.472	4693294.485	646.998	Kati 5	Shtëpi-Ndërtesë	PM
29	7511860.139	4693273.860	647.273	Kati 5	Shtëpi-Ndërtesë	PM
30	7511840.302	4693283.406	646.988	Kati 5	Shtëpi-Ndërtesë	PM
31	7511839.941	4693282.757	647.041	Kati 5	Shtëpi-Ndërtesë	PM
32	7511839.082	4693283.185	647.063	Kati 5	Shtëpi-Ndërtesë	PM
33	7511837.647	4693280.103	647.034	Kati 5	Shtëpi-Ndërtesë	PM
34	7511838.543	4693279.680	647.029	Kati 5	Shtëpi-Ndërtesë	PM
35	7511832.889	4693267.769	646.958	Kati 5	Shtëpi-Ndërtesë	PM
36	7511831.984	4693268.214	647.031	Kati 5	Shtëpi-Ndërtesë	PM
37	7511830.783	4693265.718	647.051	Kati 5	Shtëpi-Ndërtesë	PM
38	7511831.687	4693265.276	646.946	Kati 5	Shtëpi-Ndërtesë	PM

39	7511831.428	4693264.700	646.942	Kati 5	Shtëpi-Ndërtesë	PM
40	7511832.422	4693264.253	646.933	Kati 5	Shtëpi-Ndërtesë	PM
41	7511832.140	4693263.650	647.055	Kati 5	Shtëpi-Ndërtesë	PM
42	7511837.775	4693260.933	647.073	Kati 5	Shtëpi-Ndërtesë	PM
43	7511838.083	4693261.542	646.945	Kati 5	Shtëpi-Ndërtesë	PM
44	7511844.674	4693258.389	646.956	Kati 5	Shtëpi-Ndërtesë	PM
45	7511844.365	4693257.791	647.018	Kati 5	Shtëpi-Ndërtesë	PM
46	7511850.016	4693255.114	647.028	Kati 5	Shtëpi-Ndërtesë	PM
47	7511850.318	4693255.707	646.942	Kati 5	Shtëpi-Ndërtesë	PM
48	7511851.295	4693255.231	646.946	Kati 5	Shtëpi-Ndërtesë	PM
49	7511851.576	4693255.829	646.946	Kati 5	Shtëpi-Ndërtesë	PM
50	7511852.482	4693255.374	647.088	Kati 5	Shtëpi-Ndërtesë	PM
51	7511853.664	4693257.922	647.081	Kati 5	Shtëpi-Ndërtesë	PM
52	7511852.757	4693258.313	646.946	Kati 5	Shtëpi-Ndërtesë	PM
53	7511858.420	4693270.198	646.989	Kati 5	Shtëpi-Ndërtesë	PM
54	7511859.324	4693269.781	647.402	Kati 5	Shtëpi-Ndërtesë	PM
55	7511860.759	4693272.833	647.362	Kati 5	Shtëpi-Ndërtesë	PM
56	7511859.864	4693273.275	647.297	Kati 5	Shtëpi-Ndërtesë	PM

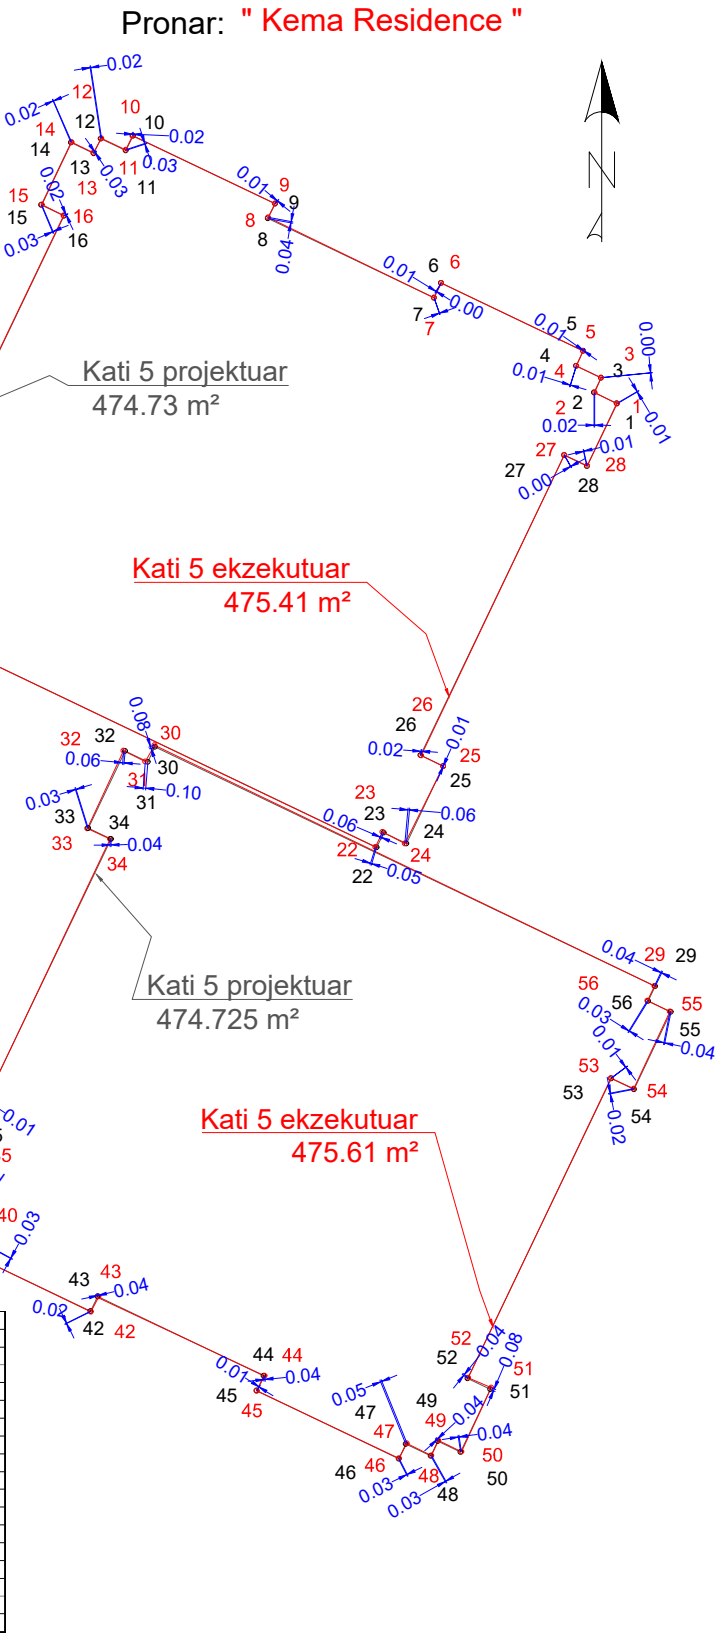

Rilevoi / Snimio: Liridon Sejdiu
(emri dhe mbiemri i gjeodetit/kompanisë/ ime i prezime geodeta/ kompanije)

Nr. i licencës / Br. licence: 140

Nënshkrimi / Potpis:

Data e rilevimit / Datum snimanja: 04/07/2026

Etazha: Kati 5

V.V.

Nënshkrimi / Potpis:

Data e aprovimit / Datum usvajanja: