

Zyra kadastrale komunale / Opštinska katastarska kancelarija: Ferizaj

Zona kadastrale / Katastarska zona: Ferizaj

Lloji i njësisë kadastrale / Vrstë katastarske jedinice : Situacion objektit



Nr. i njësisë kadastrale / Br. katastarske jedinice : 03520-0

Numri i lëndës / Broj predmeta:

Shkalla e zvoglimit / Razmera plana : 1:300

Republika e Kosovës
Republika Kosova-Republic of Kosovo
Qeveria -Vlada-Government

Ministria e Mjedisit dhe Planifikimit Hapësinor /Ministartstvo Sredine i Prostornog Planiranja/Ministry of Environment and Spatial Planning


AGJENCIA KADASTRALE E KOSOVËS/ KATASTARSKA AGENCIJA KOSOVA/ KOSOVA CADASTRAL AGENCY

Koordinatat e Kati 6 të projektuar					
Nr	Y	X	H	Kodi	Përshkrimi
1	7511858.648	4693296.964	0.000	Kati 6	Shtëpi-Ndërtesë PP
2	7511857.746	4693297.395	0.000	Kati 6	Shtëpi-Ndërtesë PP
3	7511858.026	4693297.982	0.000	Kati 6	Shtëpi-Ndërtesë PP
4	7511857.034	4693298.456	0.000	Kati 6	Shtëpi-Ndërtesë PP
5	7511857.315	4693299.402	0.000	Kati 6	Shtëpi-Ndërtesë PP
6	7511851.676	4693301.739	0.000	Kati 6	Shtëpi-Ndërtesë PP
7	7511851.396	4693301.152	0.000	Kati 6	Shtëpi-Ndërtesë PP
8	7511844.810	4693304.302	0.000	Kati 6	Shtëpi-Ndërtesë PP
9	7511845.090	4693304.888	0.000	Kati 6	Shtëpi-Ndërtesë PP
10	7511839.452	4693307.584	0.000	Kati 6	Shtëpi-Ndërtesë PP
11	7511839.171	4693306.998	0.000	Kati 6	Shtëpi-Ndërtesë PP
12	7511838.179	4693307.472	0.000	Kati 6	Shtëpi-Ndërtesë PP
13	7511837.899	4693306.886	0.000	Kati 6	Shtëpi-Ndërtesë PP
14	7511836.996	4693307.317	0.000	Kati 6	Shtëpi-Ndërtesë PP
15	7511835.810	4693304.836	0.000	Kati 6	Shtëpi-Ndërtesë PP
16	7511836.712	4693304.405	0.000	Kati 6	Shtëpi-Ndërtesë PP
17	7511831.018	4693292.497	0.000	Kati 6	Shtëpi-Ndërtesë PP
18	7511830.116	4693292.928	0.000	Kati 6	Shtëpi-Ndërtesë PP
19	7511828.649	4693289.861	0.000	Kati 6	Shtëpi-Ndërtesë PP
20	7511829.551	4693289.429	0.000	Kati 6	Shtëpi-Ndërtesë PP
21	7511829.271	4693288.843	0.000	Kati 6	Shtëpi-Ndërtesë PP
22	7511849.118	4693279.352	0.000	Kati 6	Shtëpi-Ndërtesë PP
23	7511849.398	4693279.938	0.000	Kati 6	Shtëpi-Ndërtesë PP
24	7511850.301	4693279.507	0.000	Kati 6	Shtëpi-Ndërtesë PP
25	7511851.767	4693282.574	0.000	Kati 6	Shtëpi-Ndërtesë PP
26	7511850.865	4693283.006	0.000	Kati 6	Shtëpi-Ndërtesë PP
27	7511856.560	4693294.914	0.000	Kati 6	Shtëpi-Ndërtesë PP
28	7511857.462	4693294.483	0.000	Kati 6	Shtëpi-Ndërtesë PP
29	7511860.173	4693273.844	0.000	Kati 6	Shtëpi-Ndërtesë PP
30	7511840.326	4693283.335	0.000	Kati 6	Shtëpi-Ndërtesë PP
31	7511840.045	4693282.748	0.000	Kati 6	Shtëpi-Ndërtesë PP
32	7511839.143	4693283.180	0.000	Kati 6	Shtëpi-Ndërtesë PP
33	7511837.677	4693280.112	0.000	Kati 6	Shtëpi-Ndërtesë PP
34	7511838.579	4693279.681	0.000	Kati 6	Shtëpi-Ndërtesë PP
35	7511832.884	4693267.772	0.000	Kati 6	Shtëpi-Ndërtesë PP
36	7511831.982	4693268.204	0.000	Kati 6	Shtëpi-Ndërtesë PP
37	7511830.796	4693265.723	0.000	Kati 6	Shtëpi-Ndërtesë PP
38	7511831.698	4693265.291	0.000	Kati 6	Shtëpi-Ndërtesë PP

Koordinatat e Kati 6 të ekzekutuar					
Nr	Y	X	H	Kodi	Përshkrimi
1	7511858.656	4693296.963	650.142	Kati 6	Shtëpi-Ndërtesë PM
2	7511857.752	4693297.400	650.059	Kati 6	Shtëpi-Ndërtesë PM
3	7511858.059	4693298.000	650.015	Kati 6	Shtëpi-Ndërtesë PM
4	7511857.070	4693298.481	650.103	Kati 6	Shtëpi-Ndërtesë PM
5	7511857.331	4693299.039	650.124	Kati 6	Shtëpi-Ndërtesë PM
6	7511851.649	4693301.733	650.122	Kati 6	Shtëpi-Ndërtesë PM
7	7511851.376	4693301.178	650.104	Kati 6	Shtëpi-Ndërtesë PM
8	7511844.794	4693304.297	650.017	Kati 6	Shtëpi-Ndërtesë PM
9	7511845.094	4693304.895	650.108	Kati 6	Shtëpi-Ndërtesë PM
10	7511839.437	4693307.607	650.126	Kati 6	Shtëpi-Ndërtesë PM
11	7511839.142	4693306.988	650.027	Kati 6	Shtëpi-Ndërtesë PM
12	7511838.134	4693307.476	650.011	Kati 6	Shtëpi-Ndërtesë PM
13	7511837.876	4693306.899	650.022	Kati 6	Shtëpi-Ndërtesë PM
14	7511837.023	4693307.294	650.114	Kati 6	Shtëpi-Ndërtesë PM
15	7511835.833	4693304.801	650.122	Kati 6	Shtëpi-Ndërtesë PM
16	7511836.689	4693304.400	650.009	Kati 6	Shtëpi-Ndërtesë PM
17	7511830.986	4693292.551	650.100	Kati 6	Shtëpi-Ndërtesë PM
18	7511830.087	4693292.981	650.100	Kati 6	Shtëpi-Ndërtesë PM
19	7511828.642	4693289.867	650.115	Kati 6	Shtëpi-Ndërtesë PM
20	7511829.544	4693289.449	650.028	Kati 6	Shtëpi-Ndërtesë PM
21	7511829.281	4693288.842	650.136	Kati 6	Shtëpi-Ndërtesë PM
22	7511849.074	4693279.352	650.092	Kati 6	Shtëpi-Ndërtesë PM
23	7511849.355	4693279.952	650.055	Kati 6	Shtëpi-Ndërtesë PM
24	7511850.255	4693279.513	650.125	Kati 6	Shtëpi-Ndërtesë PM
25	7511851.759	4693282.575	650.128	Kati 6	Shtëpi-Ndërtesë PM
26	7511850.867	4693283.004	650.094	Kati 6	Shtëpi-Ndërtesë PM
27	7511856.590	4693294.921	650.016	Kati 6	Shtëpi-Ndërtesë PM
28	7511857.470	4693294.461	650.144	Kati 6	Shtëpi-Ndërtesë PM
29	7511860.176	4693273.845	650.000	Kati 6	Shtëpi-Ndërtesë PM
30	7511840.283	4693283.347	649.996	Kati 6	Shtëpi-Ndërtesë PM
31	7511840.001	4693282.738	650.012	Kati 6	Shtëpi-Ndërtesë PM
32	7511839.105	4693283.187	650.150	Kati 6	Shtëpi-Ndërtesë PM
33	7511837.627	4693280.107	650.104	Kati 6	Shtëpi-Ndërtesë PM
34	7511838.502	4693279.674	650.105	Kati 6	Shtëpi-Ndërtesë PM
35	7511832.906	4693267.743	650.004	Kati 6	Shtëpi-Ndërtesë PM
36	7511831.996	4693268.180	650.137	Kati 6	Shtëpi-Ndërtesë PM
37	7511830.796	4693265.691	650.122	Kati 6	Shtëpi-Ndërtesë PM
38	7511831.705	4693265.248	650.009	Kati 6	Shtëpi-Ndërtesë PM

39	7511831.417	4693264.705	0.000	Kati 6	Shtëpi-Ndërtesë PP
40	7511832.410	4693264.230	0.000	Kati 6	Shtëpi-Ndërtesë PP
41	7511832.129	4693263.644	0.000	Kati 6	Shtëpi-Ndërtesë PP
42	7511837.768	4693260.948	0.000	Kati 6	Shtëpi-Ndërtesë PP
43	7511838.048	4693261.534	0.000	Kati 6	Shtëpi-Ndërtesë PP
44	7511844.634	4693258.385	0.000	Kati 6	Shtëpi-Ndërtesë PP
45	7511844.354	4693257.799	0.000	Kati 6	Shtëpi-Ndërtesë PP
46	7511849.992	4693255.102	0.000	Kati 6	Shtëpi-Ndërtesë PP
47	7511850.272	4693255.689	0.000	Kati 6	Shtëpi-Ndërtesë PP
48	7511851.265	4693255.214	0.000	Kati 6	Shtëpi-Ndërtesë PP
49	7511851.545	4693255.800	0.000	Kati 6	Shtëpi-Ndërtesë PP
50	7511852.447	4693255.369	0.000	Kati 6	Shtëpi-Ndërtesë PP
51	7511853.634	4693257.850	0.000	Kati 6	Shtëpi-Ndërtesë PP
52	7511852.732	4693258.281	0.000	Kati 6	Shtëpi-Ndërtesë PP
53	7511858.426	4693270.190	0.000	Kati 6	Shtëpi-Ndërtesë PP
54	7511859.328	4693269.758	0.000	Kati 6	Shtëpi-Ndërtesë PP
55	7511860.795	4693272.826	0.000	Kati 6	Shtëpi-Ndërtesë PP
56	7511859.893	4693273.257	0.000	Kati 6	Shtëpi-Ndërtesë PP

39	7511831.420	4693264.679	649.993	Kati 6	Shtëpi-Ndërtesë PM
40	7511832.399	4693264.201	650.137	Kati 6	Shtëpi-Ndërtesë PM
41	7511832.141	4693263.627	650.105	Kati 6	Shtëpi-Ndërtesë PM
42	7511837.780	4693260.930	650.111	Kati 6	Shtëpi-Ndërtesë PM
43	7511838.068	4693261.511	650.010	Kati 6	Shtëpi-Ndërtesë PM
44	7511844.607	4693258.360	650.141	Kati 6	Shtëpi-Ndërtesë PM
45	7511844.339	4693257.781	650.126	Kati 6	Shtëpi-Ndërtesë PM
46	7511849.992	4693255.089	650.136	Kati 6	Shtëpi-Ndërtesë PM
47	7511850.272	4693255.641	650.146	Kati 6	Shtëpi-Ndërtesë PM
48	7511851.257	4693255.209	650.014	Kati 6	Shtëpi-Ndërtesë PM
49	7511851.536	4693255.801	650.018	Kati 6	Shtëpi-Ndërtesë PM
50	7511852.442	4693255.356	650.110	Kati 6	Shtëpi-Ndërtesë PM
51	7511853.641	4693257.861	650.119	Kati 6	Shtëpi-Ndërtesë PM
52	7511852.737	4693258.290	650.020	Kati 6	Shtëpi-Ndërtesë PM
53	7511858.438	4693270.196	650.030	Kati 6	Shtëpi-Ndërtesë PM
54	7511859.319	4693269.740	650.106	Kati 6	Shtëpi-Ndërtesë PM
55	7511860.787	4693272.826	650.093	Kati 6	Shtëpi-Ndërtesë PM
56	7511859.897	4693273.256	650.002	Kati 6	Shtëpi-Ndërtesë PM

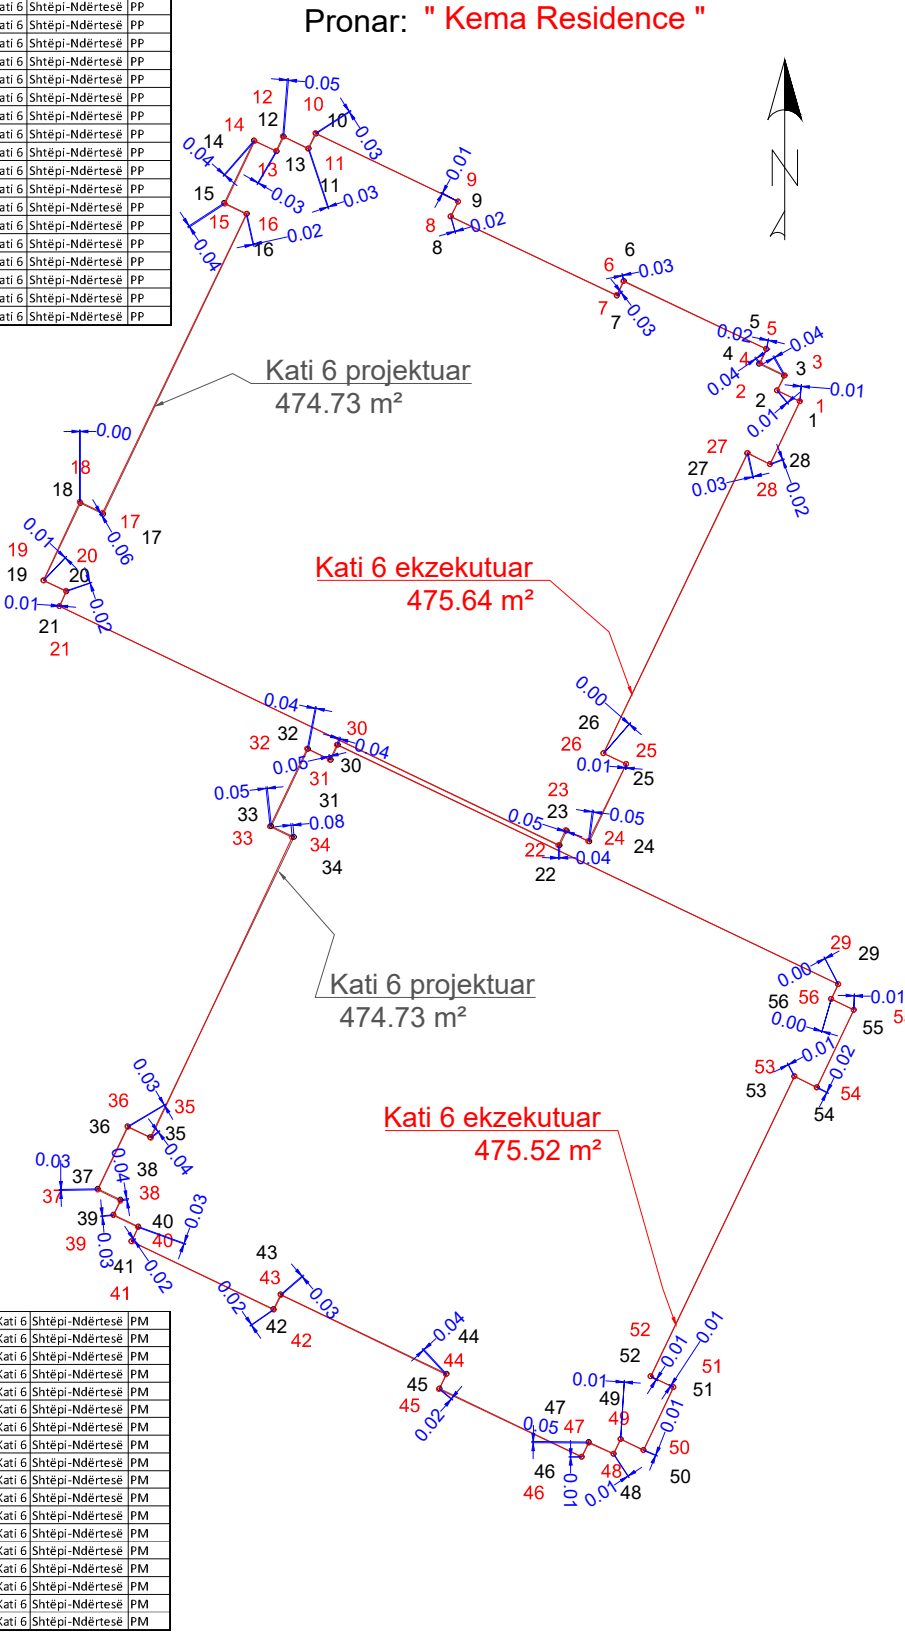

Rilevoi / Snimio: Liridon Sejdiu
(emri dhe mbiemri i gjeodetit/kompanisë/ ime i prezime geodeta/ kompanije)

Nr. i licencës / Br. licence: 140

Nënshkrimi / Potpis:

Data e rilevimit / Datum snimanja: 18/07/2026

Etazha: Kati 6

V.V.

Nënshkrimi / Potpis:

Data e aprovimit / Datum usvajanja: