

Zyra kadastrale komunale / Opštinska katastarska kancelarija: Ferizaj

Zona kadastrale / Katastarska zona: Ferizaj

Lloji i njësisë kadastrale / Vrstë katastarske jedinice : Situacion objektit



Nr. i njësisë kadastrale / Br. katastarske jedinice : 03520-0

Numri i lëndës / Broj predmeta:

Shkallë e zvoglimit / Razmëra plana : 1:300

Republika e Kosovës
Republika Kosova-Republic of Kosovo
Qeveria -Vlada-Government

Ministria e Mjedisit dhe Planifikimit Hapësinor /Ministarstvo Sredine i Prostornog Planiranja/Ministry of Environment and Spatial Planning


AGJENCIA KADASTRALE E KOSOVËS/ KATASTARSKA AGENCIJA KOSOVA/ KOSOVA CADASTRAL AGENCY

Koordinatat e Kati 7 të projektuar					
Nr	Y	X	H	Kodi	Përshkrimi
1	7511858.648	4693296.964	0.000	Kati 7	Shtëpi-Ndërtësë PP
2	7511857.746	4693297.395	0.000	Kati 7	Shtëpi-Ndërtësë PP
3	7511858.026	4693297.982	0.000	Kati 7	Shtëpi-Ndërtësë PP
4	7511857.034	4693298.456	0.000	Kati 7	Shtëpi-Ndërtësë PP
5	7511857.315	4693299.042	0.000	Kati 7	Shtëpi-Ndërtësë PP
6	7511851.676	4693301.739	0.000	Kati 7	Shtëpi-Ndërtësë PP
7	7511851.396	4693301.152	0.000	Kati 7	Shtëpi-Ndërtësë PP
8	7511844.810	4693304.302	0.000	Kati 7	Shtëpi-Ndërtësë PP
9	7511845.090	4693304.888	0.000	Kati 7	Shtëpi-Ndërtësë PP
10	7511839.452	4693307.584	0.000	Kati 7	Shtëpi-Ndërtësë PP
11	7511839.171	4693306.998	0.000	Kati 7	Shtëpi-Ndërtësë PP
12	7511838.179	4693307.472	0.000	Kati 7	Shtëpi-Ndërtësë PP
13	7511837.899	4693306.886	0.000	Kati 7	Shtëpi-Ndërtësë PP
14	7511836.996	4693307.317	0.000	Kati 7	Shtëpi-Ndërtësë PP
15	7511835.810	4693304.836	0.000	Kati 7	Shtëpi-Ndërtësë PP
16	7511836.712	4693304.405	0.000	Kati 7	Shtëpi-Ndërtësë PP
17	7511831.018	4693292.497	0.000	Kati 7	Shtëpi-Ndërtësë PP
18	7511830.116	4693292.928	0.000	Kati 7	Shtëpi-Ndërtësë PP
19	7511828.649	4693289.861	0.000	Kati 7	Shtëpi-Ndërtësë PP
20	7511829.551	4693289.429	0.000	Kati 7	Shtëpi-Ndërtësë PP
21	7511829.271	4693288.843	0.000	Kati 7	Shtëpi-Ndërtësë PP
22	7511849.118	4693279.352	0.000	Kati 7	Shtëpi-Ndërtësë PP
23	7511849.398	4693279.938	0.000	Kati 7	Shtëpi-Ndërtësë PP
24	7511850.301	4693279.507	0.000	Kati 7	Shtëpi-Ndërtësë PP
25	7511851.767	4693282.574	0.000	Kati 7	Shtëpi-Ndërtësë PP
26	7511850.865	4693283.006	0.000	Kati 7	Shtëpi-Ndërtësë PP
27	7511856.560	4693294.914	0.000	Kati 7	Shtëpi-Ndërtësë PP
28	7511857.462	4693294.483	0.000	Kati 7	Shtëpi-Ndërtësë PP
29	7511860.173	4693273.844	0.000	Kati 7	Shtëpi-Ndërtësë PP
30	7511840.326	4693283.335	0.000	Kati 7	Shtëpi-Ndërtësë PP
31	7511840.045	4693282.748	0.000	Kati 7	Shtëpi-Ndërtësë PP
32	7511839.143	4693283.180	0.000	Kati 7	Shtëpi-Ndërtësë PP
33	7511837.677	4693280.112	0.000	Kati 7	Shtëpi-Ndërtësë PP
34	7511838.579	4693279.681	0.000	Kati 7	Shtëpi-Ndërtësë PP
35	7511832.884	4693267.772	0.000	Kati 7	Shtëpi-Ndërtësë PP
36	7511831.982	4693268.204	0.000	Kati 7	Shtëpi-Ndërtësë PP
37	7511830.796	4693265.723	0.000	Kati 7	Shtëpi-Ndërtësë PP
38	7511831.698	4693265.291	0.000	Kati 7	Shtëpi-Ndërtësë PP

Koordinatat e Kati 7 të ekzekutuar					
Nr	Y	X	H	Kodi	Përshkrimi
1	7511858.666	4693296.968	653.151	Kati 7	Shtëpi-Ndërtësë PM
2	7511857.781	4693297.396	653.054	Kati 7	Shtëpi-Ndërtësë PM
3	7511858.032	4693297.977	653.049	Kati 7	Shtëpi-Ndërtësë PM
4	7511857.076	4693298.504	653.142	Kati 7	Shtëpi-Ndërtësë PM
5	7511857.345	4693299.051	653.124	Kati 7	Shtëpi-Ndërtësë PM
6	7511851.670	4693301.727	653.143	Kati 7	Shtëpi-Ndërtësë PM
7	7511851.398	4693301.184	653.128	Kati 7	Shtëpi-Ndërtësë PM
8	7511844.805	4693304.310	653.164	Kati 7	Shtëpi-Ndërtësë PM
9	7511845.068	4693304.859	653.119	Kati 7	Shtëpi-Ndërtësë PM
10	7511839.439	4693307.578	653.145	Kati 7	Shtëpi-Ndërtësë PM
11	7511839.176	4693307.026	653.142	Kati 7	Shtëpi-Ndërtësë PM
12	7511838.186	4693307.477	653.042	Kati 7	Shtëpi-Ndërtësë PM
13	7511837.875	4693306.924	653.141	Kati 7	Shtëpi-Ndërtësë PM
14	7511837.051	4693307.312	653.135	Kati 7	Shtëpi-Ndërtësë PM
15	7511835.848	4693304.804	653.189	Kati 7	Shtëpi-Ndërtësë PM
16	7511836.673	4693304.411	653.151	Kati 7	Shtëpi-Ndërtësë PM
17	7511831.050	4693292.498	653.044	Kati 7	Shtëpi-Ndërtësë PM
18	7511830.136	4693292.926	653.146	Kati 7	Shtëpi-Ndërtësë PM
19	7511828.659	4693289.880	653.154	Kati 7	Shtëpi-Ndërtësë PM
20	7511829.531	4693289.442	653.130	Kati 7	Shtëpi-Ndërtësë PM
21	7511829.256	4693288.844	653.071	Kati 7	Shtëpi-Ndërtësë PM
22	7511849.092	4693279.355	653.027	Kati 7	Shtëpi-Ndërtësë PM
23	7511849.400	4693279.924	653.145	Kati 7	Shtëpi-Ndërtësë PM
24	7511850.267	4693279.508	653.144	Kati 7	Shtëpi-Ndërtësë PM
25	7511851.755	4693282.573	653.140	Kati 7	Shtëpi-Ndërtësë PM
26	7511850.867	4693283.000	653.137	Kati 7	Shtëpi-Ndërtësë PM
27	7511856.592	4693294.906	653.367	Kati 7	Shtëpi-Ndërtësë PM
28	7511857.485	4693294.501	653.154	Kati 7	Shtëpi-Ndërtësë PM
29	7511860.173	4693273.849	653.043	Kati 7	Shtëpi-Ndërtësë PM
30	7511840.357	4693283.340	653.052	Kati 7	Shtëpi-Ndërtësë PM
31	7511840.027	4693282.758	653.168	Kati 7	Shtëpi-Ndërtësë PM
32	7511839.158	4693283.186	653.162	Kati 7	Shtëpi-Ndërtësë PM
33	7511837.671	4693280.085	653.160	Kati 7	Shtëpi-Ndërtësë PM
34	7511838.602	4693279.653	653.061	Kati 7	Shtëpi-Ndërtësë PM
35	7511832.902	4693267.774	653.049	Kati 7	Shtëpi-Ndërtësë PM
36	7511831.994	4693268.216	653.143	Kati 7	Shtëpi-Ndërtësë PM
37	7511830.797	4693265.720	653.144	Kati 7	Shtëpi-Ndërtësë PM
38	7511831.709	4693265.288	653.052	Kati 7	Shtëpi-Ndërtësë PM

39	7511831.417	4693264.705	0.000	Kati 7	Shtëpi-Ndërtësë PP
40	7511832.410	4693264.230	0.000	Kati 7	Shtëpi-Ndërtësë PP
41	7511832.129	4693263.644	0.000	Kati 7	Shtëpi-Ndërtësë PP
42	7511837.768	4693260.948	0.000	Kati 7	Shtëpi-Ndërtësë PP
43	7511838.048	4693261.534	0.000	Kati 7	Shtëpi-Ndërtësë PP
44	7511844.634	4693258.385	0.000	Kati 7	Shtëpi-Ndërtësë PP
45	7511844.354	4693257.799	0.000	Kati 7	Shtëpi-Ndërtësë PP
46	7511849.992	4693255.102	0.000	Kati 7	Shtëpi-Ndërtësë PP
47	7511850.272	4693255.689	0.000	Kati 7	Shtëpi-Ndërtësë PP
48	7511851.265	4693255.214	0.000	Kati 7	Shtëpi-Ndërtësë PP
49	7511851.545	4693255.800	0.000	Kati 7	Shtëpi-Ndërtësë PP
50	7511852.447	4693255.369	0.000	Kati 7	Shtëpi-Ndërtësë PP
51	7511853.634	4693257.850	0.000	Kati 7	Shtëpi-Ndërtësë PP
52	7511852.732	4693258.281	0.000	Kati 7	Shtëpi-Ndërtësë PP
53	7511858.426	4693270.190	0.000	Kati 7	Shtëpi-Ndërtësë PP
54	7511859.328	4693269.758	0.000	Kati 7	Shtëpi-Ndërtësë PP
55	7511860.795	4693272.826	0.000	Kati 7	Shtëpi-Ndërtësë PP
56	7511859.893	4693273.257	0.000	Kati 7	Shtëpi-Ndërtësë PP

39	7511831.421	4693264.707	653.043	Kati 7	Shtëpi-Ndërtësë PM
40	7511832.402	4693264.218	653.178	Kati 7	Shtëpi-Ndërtësë PM
41	7511832.132	4693263.649	653.142	Kati 7	Shtëpi-Ndërtësë PM
42	7511837.776	4693260.936	653.155	Kati 7	Shtëpi-Ndërtësë PM
43	7511838.069	4693261.522	653.047	Kati 7	Shtëpi-Ndërtësë PM
44	7511844.592	4693258.388	653.165	Kati 7	Shtëpi-Ndërtësë PM
45	7511844.330	4693257.795	653.172	Kati 7	Shtëpi-Ndërtësë PM
46	7511849.982	4693255.096	653.152	Kati 7	Shtëpi-Ndërtësë PM
47	7511850.256	4693255.637	653.149	Kati 7	Shtëpi-Ndërtësë PM
48	7511851.248	4693255.212	653.058	Kati 7	Shtëpi-Ndërtësë PM
49	7511851.543	4693255.781	653.066	Kati 7	Shtëpi-Ndërtësë PM
50	7511852.441	4693255.351	653.155	Kati 7	Shtëpi-Ndërtësë PM
51	7511853.625	4693257.855	653.182	Kati 7	Shtëpi-Ndërtësë PM
52	7511852.748	4693258.277	653.150	Kati 7	Shtëpi-Ndërtësë PM
53	7511858.402	4693270.184	653.059	Kati 7	Shtëpi-Ndërtësë PM
54	7511859.324	4693269.744	653.152	Kati 7	Shtëpi-Ndërtësë PM
55	7511860.778	4693272.828	653.137	Kati 7	Shtëpi-Ndërtësë PM
56	7511859.886	4693273.253	653.057	Kati 7	Shtëpi-Ndërtësë PM

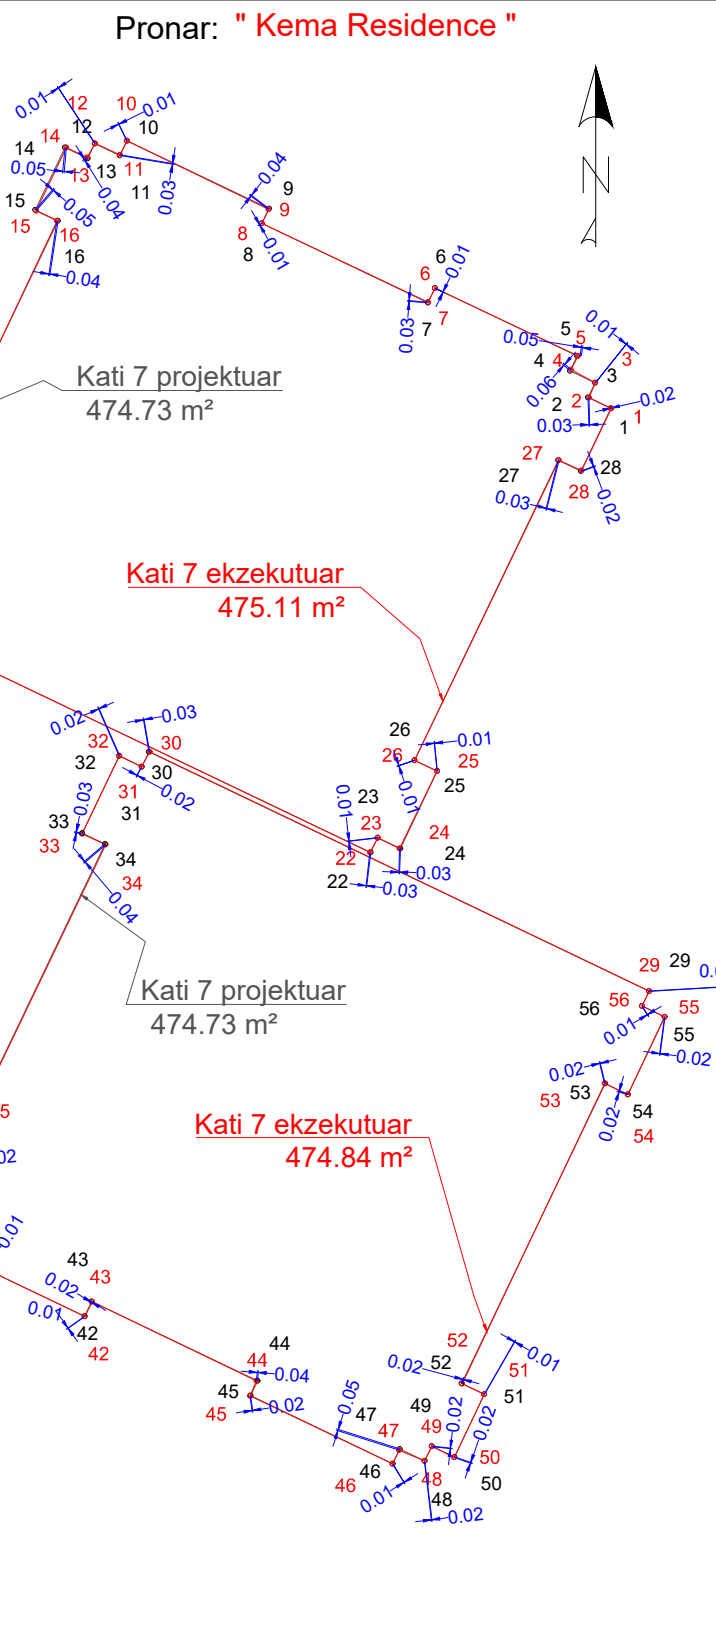

Rilevoi / Snimio: Liridon Sejdiu
(emri dhe mbiemri i gjeodetit/kompanisë/ ime i prezime geodeta/ kompanije)

Nr. i licencës / Br. licence: 140

Nënshkrimi / Potpis:

Data e rilevimit / Datum snimanja: 31/07/2026

Etazha: Kati 7

Nënshkrimi / Potpis:

Data e aprovimit / Datum usvajanja: