




Republika e Kosovës
Republika Kosova-Republic of Kosova
Qeveria -Vlada-Government
Ministria e Mjedisit dhe Planifikimit Hapësinor /Ministartstvo Sredine i Prostornog Planiranja/Ministry of Environment and Spatial Planning
AGJENCIA KADASTRALE E KOSOVËS/ KATASTARSKA AGENCIJA KOSOVA/ KOSOVA CADASTRAL AGENCY

Koordinatat e Kati 4 të projektuar					
Nr	Y	X	H	Kodi	Përshkrimi
1	7511858.648	4693296.964	0.000	Kati 4	Shtëpi-Ndërtesë
2	7511857.746	4693297.395	0.000	Kati 4	Shtëpi-Ndërtesë
3	7511858.026	4693297.982	0.000	Kati 4	Shtëpi-Ndërtesë
4	7511857.034	4693298.456	0.000	Kati 4	Shtëpi-Ndërtesë
5	7511857.315	4693299.042	0.000	Kati 4	Shtëpi-Ndërtesë
6	7511851.676	4693301.739	0.000	Kati 4	Shtëpi-Ndërtesë
7	7511851.396	4693301.152	0.000	Kati 4	Shtëpi-Ndërtesë
8	7511844.810	4693304.302	0.000	Kati 4	Shtëpi-Ndërtesë
9	7511845.090	4693304.888	0.000	Kati 4	Shtëpi-Ndërtesë
10	7511839.452	4693307.584	0.000	Kati 4	Shtëpi-Ndërtesë
11	7511839.171	4693306.998	0.000	Kati 4	Shtëpi-Ndërtesë
12	7511838.179	4693307.472	0.000	Kati 4	Shtëpi-Ndërtesë
13	7511837.899	4693306.886	0.000	Kati 4	Shtëpi-Ndërtesë
14	7511836.996	4693307.317	0.000	Kati 4	Shtëpi-Ndërtesë
15	7511835.810	4693304.836	0.000	Kati 4	Shtëpi-Ndërtesë
16	7511836.712	4693304.405	0.000	Kati 4	Shtëpi-Ndërtesë
17	7511831.018	4693292.497	0.000	Kati 4	Shtëpi-Ndërtesë
18	7511830.116	4693292.928	0.000	Kati 4	Shtëpi-Ndërtesë
19	7511828.649	4693289.861	0.000	Kati 4	Shtëpi-Ndërtesë
20	7511829.551	4693289.429	0.000	Kati 4	Shtëpi-Ndërtesë
21	7511829.271	4693288.843	0.000	Kati 4	Shtëpi-Ndërtesë
22	7511849.118	4693279.352	0.000	Kati 4	Shtëpi-Ndërtesë
23	7511849.398	4693279.938	0.000	Kati 4	Shtëpi-Ndërtesë
24	7511850.301	4693279.507	0.000	Kati 4	Shtëpi-Ndërtesë
25	7511851.767	4693282.574	0.000	Kati 4	Shtëpi-Ndërtesë
26	7511850.865	4693283.006	0.000	Kati 4	Shtëpi-Ndërtesë
27	7511856.560	4693294.914	0.000	Kati 4	Shtëpi-Ndërtesë
28	7511857.462	4693294.483	0.000	Kati 4	Shtëpi-Ndërtesë
29	7511860.173	4693273.844	0.000	Kati 4	Shtëpi-Ndërtesë
30	7511835.770	4693285.513	0.000	Kati 4	Shtëpi-Ndërtesë
31	7511829.881	4693273.199	0.000	Kati 4	Shtëpi-Ndërtesë
32	7511834.437	4693271.020	0.000	Kati 4	Shtëpi-Ndërtesë
33	7511830.796	4693265.723	0.000	Kati 4	Shtëpi-Ndërtesë
34	7511831.698	4693265.291	0.000	Kati 4	Shtëpi-Ndërtesë
35	7511831.417	4693264.705	0.000	Kati 4	Shtëpi-Ndërtesë

Koordinatat e Kati 4 të ekzekutuar					
Nr	Y	X	H	Kodi	Përshkrimi
1	7511858.670	4693296.945	643.920	Kati 4	Shtëpi-Ndërtesë
2	7511857.774	4693297.384	643.922	Kati 4	Shtëpi-Ndërtesë
3	7511858.027	4693297.956	643.917	Kati 4	Shtëpi-Ndërtesë
4	7511857.050	4693298.472	643.927	Kati 4	Shtëpi-Ndërtesë
5	7511857.318	4693299.014	643.912	Kati 4	Shtëpi-Ndërtesë
6	7511851.690	4693301.739	644.008	Kati 4	Shtëpi-Ndërtesë
7	7511851.416	4693301.159	643.915	Kati 4	Shtëpi-Ndërtesë
8	7511844.825	4693304.314	643.998	Kati 4	Shtëpi-Ndërtesë
9	7511845.092	4693304.879	643.997	Kati 4	Shtëpi-Ndërtesë
10	7511839.452	4693307.625	643.999	Kati 4	Shtëpi-Ndërtesë
11	7511839.189	4693307.055	643.999	Kati 4	Shtëpi-Ndërtesë
12	7511838.203	4693307.476	643.927	Kati 4	Shtëpi-Ndërtesë
13	7511837.885	4693306.883	643.942	Kati 4	Shtëpi-Ndërtesë
14	7511836.987	4693307.352	643.942	Kati 4	Shtëpi-Ndërtesë
15	7511835.798	4693304.886	644.013	Kati 4	Shtëpi-Ndërtesë
16	7511836.668	4693304.418	643.977	Kati 4	Shtëpi-Ndërtesë
17	7511830.991	4693292.523	644.013	Kati 4	Shtëpi-Ndërtesë
18	7511830.124	4693292.947	644.019	Kati 4	Shtëpi-Ndërtesë
19	7511828.650	4693289.857	644.020	Kati 4	Shtëpi-Ndërtesë
20	7511829.529	4693289.427	644.025	Kati 4	Shtëpi-Ndërtesë
21	7511829.261	4693288.847	643.878	Kati 4	Shtëpi-Ndërtesë
22	7511849.089	4693279.364	643.937	Kati 4	Shtëpi-Ndërtesë
23	7511849.395	4693279.936	643.981	Kati 4	Shtëpi-Ndërtesë
24	7511850.273	4693279.497	644.017	Kati 4	Shtëpi-Ndërtesë
25	7511851.775	4693282.568	643.926	Kati 4	Shtëpi-Ndërtesë
26	7511850.847	4693282.999	643.918	Kati 4	Shtëpi-Ndërtesë
27	7511856.588	4693294.908	643.913	Kati 4	Shtëpi-Ndërtesë
28	7511857.444	4693294.444	643.923	Kati 4	Shtëpi-Ndërtesë
29	7511860.178	4693273.842	643.913	Kati 4	Shtëpi-Ndërtesë
30	7511834.905	4693286.022	644.016	Kati 4	Shtëpi-Ndërtesë
31	7511828.547	4693272.765	644.025	Kati 4	Shtëpi-Ndërtesë
32	7511833.100	4693270.527	644.010	Kati 4	Shtëpi-Ndërtesë
33	7511830.791	4693265.718	644.018	Kati 4	Shtëpi-Ndërtesë
34	7511831.696	4693265.276	644.034	Kati 4	Shtëpi-Ndërtesë
35	7511831.414	4693264.721	644.006	Kati 4	Shtëpi-Ndërtesë

36	7511832.410	4693264.230	0.000	Kati 4	Shtëpi-Ndërtesë
37	7511832.129	4693263.644	0.000	Kati 4	Shtëpi-Ndërtesë
38	7511837.768	4693260.948	0.000	Kati 4	Shtëpi-Ndërtesë
39	7511838.048	4693261.534	0.000	Kati 4	Shtëpi-Ndërtesë
40	7511844.634	4693258.385	0.000	Kati 4	Shtëpi-Ndërtesë
41	7511844.354	4693257.799	0.000	Kati 4	Shtëpi-Ndërtesë
42	7511849.992	4693255.102	0.000	Kati 4	Shtëpi-Ndërtesë
43	7511850.272	4693255.689	0.000	Kati 4	Shtëpi-Ndërtesë
44	7511851.265	4693255.214	0.000	Kati 4	Shtëpi-Ndërtesë
45	7511851.545	4693255.800	0.000	Kati 4	Shtëpi-Ndërtesë
46	7511852.447	4693255.369	0.000	Kati 4	Shtëpi-Ndërtesë
47	7511853.634	4693257.850	0.000	Kati 4	Shtëpi-Ndërtesë
48	7511852.732	4693258.281	0.000	Kati 4	Shtëpi-Ndërtesë
49	7511858.426	4693270.190	0.000	Kati 4	Shtëpi-Ndërtesë
50	7511859.328	4693269.758	0.000	Kati 4	Shtëpi-Ndërtesë
51	7511860.795	4693272.826	0.000	Kati 4	Shtëpi-Ndërtesë
52	7511859.893	4693273.257	0.000	Kati 4	Shtëpi-Ndërtesë
53	7511831.982	4693268.204	0.000	Kati 4	Shtëpi-Ndërtesë
54	7511832.884	4693267.772	0.000	Kati 4	Shtëpi-Ndërtesë

36	7511832.418	4693264.191	644.020	Kati 4	Shtëpi-Ndërtesë
37	7511832.139	4693263.644	644.020	Kati 4	Shtëpi-Ndërtesë
38	7511837.782	4693260.929	644.017	Kati 4	Shtëpi-Ndërtesë
39	7511838.075	4693261.486	644.011	Kati 4	Shtëpi-Ndërtesë
40	7511844.651	4693258.355	643.997	Kati 4	Shtëpi-Ndërtesë
41	7511844.358	4693257.800	644.026	Kati 4	Shtëpi-Ndërtesë
42	7511850.019	4693255.096	644.030	Kati 4	Shtëpi-Ndërtesë
43	7511850.297	4693255.666	643.938	Kati 4	Shtëpi-Ndërtesë
44	7511851.276	4693255.200	643.936	Kati 4	Shtëpi-Ndërtesë
45	7511851.553	4693255.810	643.935	Kati 4	Shtëpi-Ndërtesë
46	7511852.469	4693255.348	644.030	Kati 4	Shtëpi-Ndërtesë
47	7511853.658	4693257.827	644.039	Kati 4	Shtëpi-Ndërtesë
48	7511852.751	4693258.282	643.928	Kati 4	Shtëpi-Ndërtesë
49	7511858.451	4693270.159	643.931	Kati 4	Shtëpi-Ndërtesë
50	7511859.342	4693269.734	644.028	Kati 4	Shtëpi-Ndërtesë
51	7511860.795	4693272.841	643.948	Kati 4	Shtëpi-Ndërtesë
52	7511859.917	4693273.293	643.921	Kati 4	Shtëpi-Ndërtesë

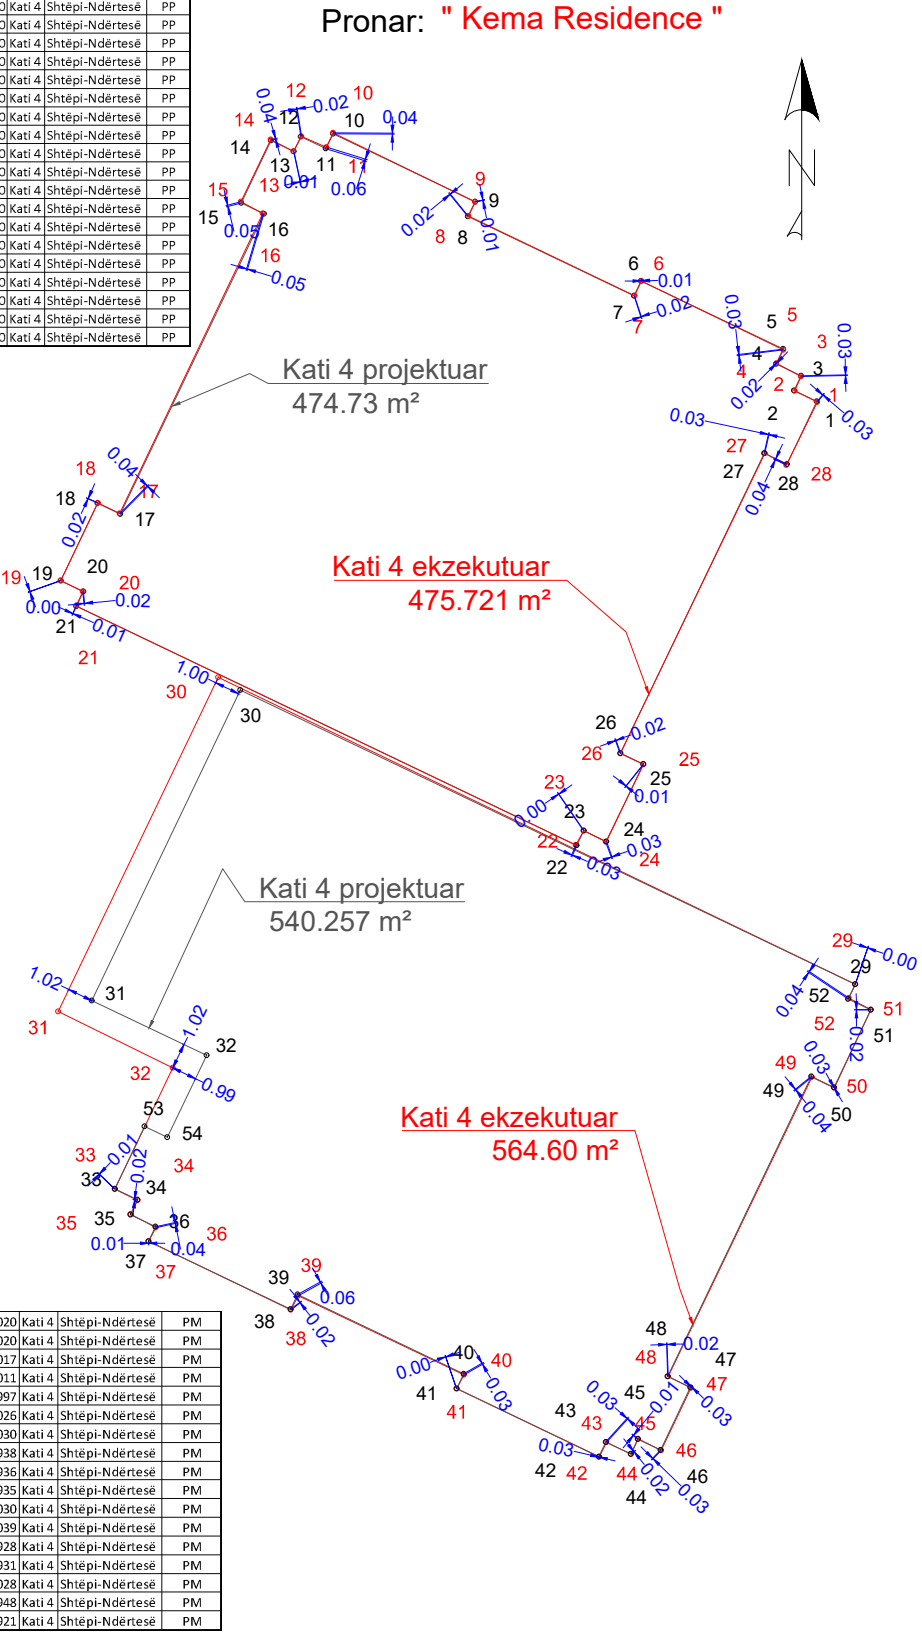

Rilevoi / Snimio: Liridon Sejdiu
(emri dhe mbiemri i gjeodetit/kompanisë/ ime i prezime gjeodeta/ kompanije)

Nr. i licencës / Br. licence: 140

Nënshkrimi / Potpis:

Data e rielimit / Datum snimanja: 06/06/2026

Etazha: Kati 4

Nënshkrimi / Potpis:

Data e aprovimit / Datum usvajanja: