Zyra kadastrale komunale / Opštinska katastarska kancelarija: Ferizaj

Zona kadastrale / Katastarska zona: Ferizaj

Lloji i njësisë kadastrale / Vrsta katastarske jedinice : Situacion objektit

Nr. i njësisë kadastrale / Br. katastarske jedinice : 03520-0

Numri i lëndës / Broj predmeta:

Shkalla e zvoglimit / Razmera plana : 1:250

Republika e Kosovës

Republika Kosova-Republic of Kosova

Qeveria -Vlada-Government

Ministria e Mjedisit dhe Planifikimit Hapësinor /Ministarstvo Sredine i Prostornog Planiranja/Ministry of Environment and Spatial Planning

AGJENCIA KADASTRALE E KOSOVËS/ KATASTARSKA AGECIJA KOSOVA/ KOSOVA CADASTRAL AGENCY

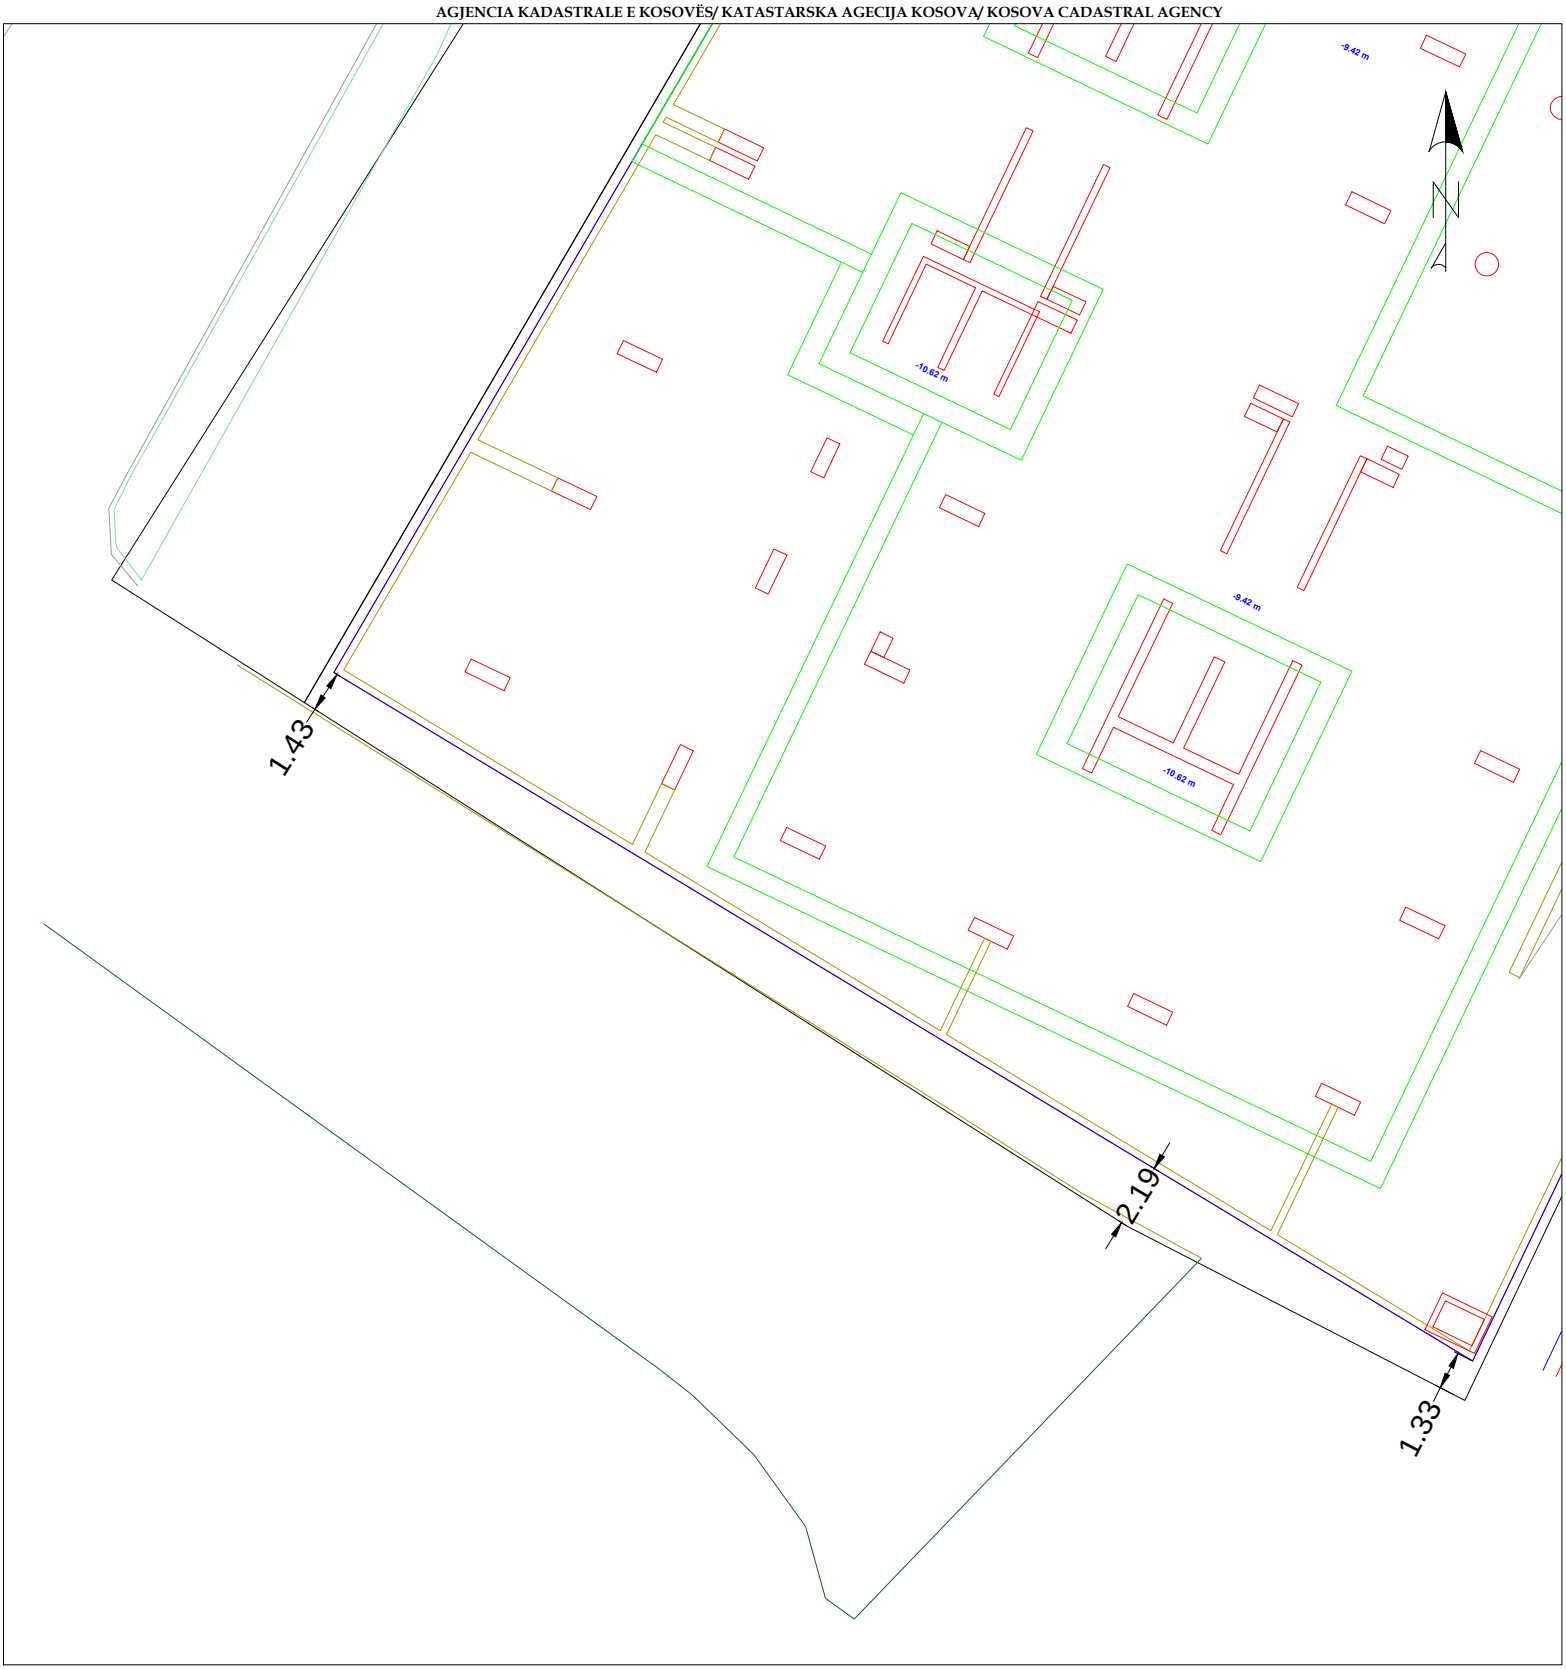

Rilevoi / Snimio: LIRIDON SEJDIU

(emri dhe mbiemri i gjeodetit/kompanisë/ ime i prezime geodeta/ kompanije)

Nr. i licencës / Br. licence: 140

Nënshkrimi / Potpis:

Data e rilevimit / Datum snimanja: 23.12.2025

V.V.

Rilevoi / Snimio:

(emri dhe mbiemri i gjeodetit/kompanisë/ ime i prezime geodeta/ kompanije)

Nënshkrimi / Potpis:

Data e aprovimit / Datum usvajanja: