

Zyra kadastrale komunale / Opštinska katastarska kancelarija: Ferizaj

Zona kadastrale / Katastarska zona: Ferizaj

Lloji i njësish kadastrale / Vrsta katastarske jedinice : Situacion objektit



Nr. i njësish kadastrale / Br. katastarske jedinice : 03520-0

Numri i lëndës / Broj predmeta:


Shkalla e zvoglimit / Razmera plana : 1:300

Republika e Kosovës
Republika Kosova-Republic of Kosova
Qeveria -Vlada-Government

Ministria e Mjedisit dhe Planifikimit Hapësinor /Ministarstvo Sredine i Prostornog Planiranja/Ministry of Environment and Spatial Planning
AGJENCIA KADASTRALE E KOSOVËS/ KATASTARSKA AGENCIJA KOSOV./ KOSOVA CADASTRAL AGENCY

Koordinatat e Kati 5 të projektuar											
Nr	Y	X	H	Kodi	Përshkrimi	Burimi					
1	7511858.648	4693296.954	0.000	Kati 5	Shtëpi-Ndërtesë	PP	39	7511831.417	4693264.705	0.000	Kati 5 Shtëpi-Ndërtesë PP
2	7511857.746	4693297.395	0.000	Kati 5	Shtëpi-Ndërtesë	PP	40	7511832.410	4693264.230	0.000	Kati 5 Shtëpi-Ndërtesë PP
3	7511858.026	4693297.982	0.000	Kati 5	Shtëpi-Ndërtesë	PP	41	7511832.129	4693263.644	0.000	Kati 5 Shtëpi-Ndërtesë PP
4	7511857.034	4693298.456	0.000	Kati 5	Shtëpi-Ndërtesë	PP	42	7511837.768	4693260.948	0.000	Kati 5 Shtëpi-Ndërtesë PP
5	7511857.315	4693299.042	0.000	Kati 5	Shtëpi-Ndërtesë	PP	43	7511838.048	4693261.534	0.000	Kati 5 Shtëpi-Ndërtesë PP
6	7511851.676	4693301.739	0.000	Kati 5	Shtëpi-Ndërtesë	PP	44	7511844.634	4693258.385	0.000	Kati 5 Shtëpi-Ndërtesë PP
7	7511851.396	4693301.152	0.000	Kati 5	Shtëpi-Ndërtesë	PP	45	7511844.354	4693257.799	0.000	Kati 5 Shtëpi-Ndërtesë PP
8	7511844.810	4693304.302	0.000	Kati 5	Shtëpi-Ndërtesë	PP	46	7511849.992	4693255.102	0.000	Kati 5 Shtëpi-Ndërtesë PP
9	7511845.090	4693304.888	0.000	Kati 5	Shtëpi-Ndërtesë	PP	47	7511850.272	4693255.689	0.000	Kati 5 Shtëpi-Ndërtesë PP
10	7511839.452	4693307.584	0.000	Kati 5	Shtëpi-Ndërtesë	PP	48	7511851.265	4693255.214	0.000	Kati 5 Shtëpi-Ndërtesë PP
11	7511839.171	4693306.998	0.000	Kati 5	Shtëpi-Ndërtesë	PP	49	7511851.545	4693255.800	0.000	Kati 5 Shtëpi-Ndërtesë PP
12	7511838.179	4693307.472	0.000	Kati 5	Shtëpi-Ndërtesë	PP	50	7511852.447	4693255.369	0.000	Kati 5 Shtëpi-Ndërtesë PP
13	7511837.899	4693306.886	0.000	Kati 5	Shtëpi-Ndërtesë	PP	51	7511853.634	4693257.850	0.000	Kati 5 Shtëpi-Ndërtesë PP
14	7511836.996	4693307.317	0.000	Kati 5	Shtëpi-Ndërtesë	PP	52	7511852.732	4693258.281	0.000	Kati 5 Shtëpi-Ndërtesë PP
15	7511835.810	4693304.836	0.000	Kati 5	Shtëpi-Ndërtesë	PP	53	7511858.426	4693270.190	0.000	Kati 5 Shtëpi-Ndërtesë PP
16	7511836.712	4693304.405	0.000	Kati 5	Shtëpi-Ndërtesë	PP	54	7511859.328	4693269.758	0.000	Kati 5 Shtëpi-Ndërtesë PP
17	7511831.018	4693292.497	0.000	Kati 5	Shtëpi-Ndërtesë	PP	55	7511860.795	4693272.826	0.000	Kati 5 Shtëpi-Ndërtesë PP
18	7511830.116	4693292.928	0.000	Kati 5	Shtëpi-Ndërtesë	PP	56	7511859.893	4693273.257	0.000	Kati 5 Shtëpi-Ndërtesë PP
19	7511828.649	4693289.861	0.000	Kati 5	Shtëpi-Ndërtesë	PP					
20	7511829.551	4693289.429	0.000	Kati 5	Shtëpi-Ndërtesë	PP					
21	7511829.271	4693288.843	0.000	Kati 5	Shtëpi-Ndërtesë	PP					
22	7511849.118	4693279.352	0.000	Kati 5	Shtëpi-Ndërtesë	PP					
23	7511849.398	4693279.938	0.000	Kati 5	Shtëpi-Ndërtesë	PP					
24	7511850.301	4693279.507	0.000	Kati 5	Shtëpi-Ndërtesë	PP					
25	7511851.767	4693282.574	0.000	Kati 5	Shtëpi-Ndërtesë	PP					
26	7511850.865	4693283.006	0.000	Kati 5	Shtëpi-Ndërtesë	PP					
27	7511856.560	4693294.914	0.000	Kati 5	Shtëpi-Ndërtesë	PP					
28	7511857.462	4693294.483	0.000	Kati 5	Shtëpi-Ndërtesë	PP					
29	7511860.173	4693273.844	0.000	Kati 5	Shtëpi-Ndërtesë	PP					
30	7511840.326	4693283.335	0.000	Kati 5	Shtëpi-Ndërtesë	PP					
31	7511840.045	4693282.748	0.000	Kati 5	Shtëpi-Ndërtesë	PP					
32	7511839.143	4693283.180	0.000	Kati 5	Shtëpi-Ndërtesë	PP					
33	7511837.577	4693280.112	0.000	Kati 5	Shtëpi-Ndërtesë	PP					
34	7511838.579	4693279.681	0.000	Kati 5	Shtëpi-Ndërtesë	PP					
35	7511832.884	4693267.772	0.000	Kati 5	Shtëpi-Ndërtesë	PP					
36	7511831.982	4693268.204	0.000	Kati 5	Shtëpi-Ndërtesë	PP					
37	7511830.796	4693265.723	0.000	Kati 5	Shtëpi-Ndërtesë	PP					
38	7511831.698	4693265.291	0.000	Kati 5	Shtëpi-Ndërtesë	PP					

Koordinatat e Kati 5 të ekzekutuar											
Nr	Y	X	H	Kodi	Përshkrimi	Burimi					
1	7511858.655	4693296.952	647.009	Kati 5	Shtëpi-Ndërtesë	PM	39	7511831.428	4693264.700	646.942	Kati 5 Shtëpi-Ndërtesë PM
2	7511857.768	4693297.395	647.002	Kati 5	Shtëpi-Ndërtesë	PM	40	7511832.422	4693264.253	646.933	Kati 5 Shtëpi-Ndërtesë PM
3	7511858.026	4693297.986	646.999	Kati 5	Shtëpi-Ndërtesë	PM	41	7511832.140	4693263.650	647.055	Kati 5 Shtëpi-Ndërtesë PM
4	7511857.044	4693298.453	647.011	Kati 5	Shtëpi-Ndërtesë	PM	42	7511837.775	4693260.933	647.073	Kati 5 Shtëpi-Ndërtesë PM
5	7511857.308	4693299.047	647.008	Kati 5	Shtëpi-Ndërtesë	PM	43	7511838.083	4693261.542	646.945	Kati 5 Shtëpi-Ndërtesë PM
6	7511851.682	4693301.735	646.994	Kati 5	Shtëpi-Ndërtesë	PM	44	7511844.674	4693258.389	646.956	Kati 5 Shtëpi-Ndërtesë PM
7	7511851.392	4693301.151	646.988	Kati 5	Shtëpi-Ndërtesë	PM	45	7511844.365	4693257.791	647.018	Kati 5 Shtëpi-Ndërtesë PM
8	7511844.818	4693304.345	647.092	Kati 5	Shtëpi-Ndërtesë	PM	46	7511850.016	4693255.114	647.028	Kati 5 Shtëpi-Ndërtesë PM
9	7511845.083	4693304.894	646.986	Kati 5	Shtëpi-Ndërtesë	PM	47	7511850.318	4693255.707	646.942	Kati 5 Shtëpi-Ndërtesë PM
10	7511839.434	4693307.585	646.987	Kati 5	Shtëpi-Ndërtesë	PM	48	7511851.295	4693255.231	646.946	Kati 5 Shtëpi-Ndërtesë PM
11	7511839.161	4693307.029	647.001	Kati 5	Shtëpi-Ndërtesë	PM	49	7511851.576	4693255.829	646.946	Kati 5 Shtëpi-Ndërtesë PM
12	7511838.203	4693307.476	643.937	Kati 5	Shtëpi-Ndërtesë	PM	50	7511852.482	4693255.374	647.088	Kati 5 Shtëpi-Ndërtesë PM
13	7511837.881	4693306.912	647.002	Kati 5	Shtëpi-Ndërtesë	PM	51	7511853.664	4693257.922	647.081	Kati 5 Shtëpi-Ndërtesë PM
14	7511837.014	4693307.325	647.008	Kati 5	Shtëpi-Ndërtesë	PM	52	7511852.757	4693258.313	646.946	Kati 5 Shtëpi-Ndërtesë PM
15	7511835.835	4693304.647	647.139	Kati 5	Shtëpi-Ndërtesë	PM	53	7511858.420	4693270.198	646.989	Kati 5 Shtëpi-Ndërtesë PM
16	7511836.705	4693304.421	646.994	Kati 5	Shtëpi-Ndërtesë	PM	54	7511859.324	4693269.781	647.402	Kati 5 Shtëpi-Ndërtesë PM
17	7511830.998	4693292.513	646.989	Kati 5	Shtëpi-Ndërtesë	PM	55	7511860.759	4693272.833	647.362	Kati 5 Shtëpi-Ndërtesë PM
18	7511830.085	4693292.949	647.109	Kati 5	Shtëpi-Ndërtesë	PM	56	7511859.864	4693273.275	647.297	Kati 5 Shtëpi-Ndërtesë PM
19	7511828.640	4693289.850	647.096	Kati 5	Shtëpi-Ndërtesë	PM					
20	7511829.521	4693289.432	647.010	Kati 5	Shtëpi-Ndërtesë	PM					
21	7511829.255	4693288.845	647.014	Kati 5	Shtëpi-Ndërtesë	PM					
22	7511849.072	4693279.366	647.044	Kati 5	Shtëpi-Ndërtesë	PM					
23	7511849.347	4693279.960	647.006	Kati 5	Shtëpi-Ndërtesë	PM					
24	7511850.242	4693279.512	647.112	Kati 5	Shtëpi-Ndërtesë	PM					
25	7511851.765	4693282.599	647.136	Kati 5	Shtëpi-Ndërtesë	PM					
26	7511850.889	4693283.004	647.139	Kati 5	Shtëpi-Ndërtesë	PM					
27	7511856.563	4693294.916	646.999	Kati 5	Shtëpi-Ndërtesë	PM					
28	7511857.472	4693294.485	646.996	Kati 5	Shtëpi-Ndërtesë	PM					
29	7511860.139	4693273.860	647.273	Kati 5	Shtëpi-Ndërtesë	PM					
30	7511840.302	4693283.406	646.988	Kati 5	Shtëpi-Ndërtesë	PM					
31	7511839.941	4693282.757	647.041	Kati 5	Shtëpi-Ndërtesë	PM					
32	7511839.082	4693283.185	647.063	Kati 5	Shtëpi-Ndërtesë	PM					
33	7511837.647	4693280.103	647.034	Kati 5	Shtëpi-Ndërtesë	PM					
34	7511838.543	4693279.680	647.029	Kati 5	Shtëpi-Ndërtesë	PM					
35	7511832.889	4693267.769	646.958	Kati 5	Shtëpi-Ndërtesë	PM					
36	7511831.984	4693268.214	647.031	Kati 5	Shtëpi-Ndërtesë	PM					
37	7511830.783	4693265.718	647.061	Kati 5	Shtëpi-Ndërtesë	PM					
38	7511831.687	4693265.276	646.946	Kati 5	Shtëpi-Ndërtesë	PM					

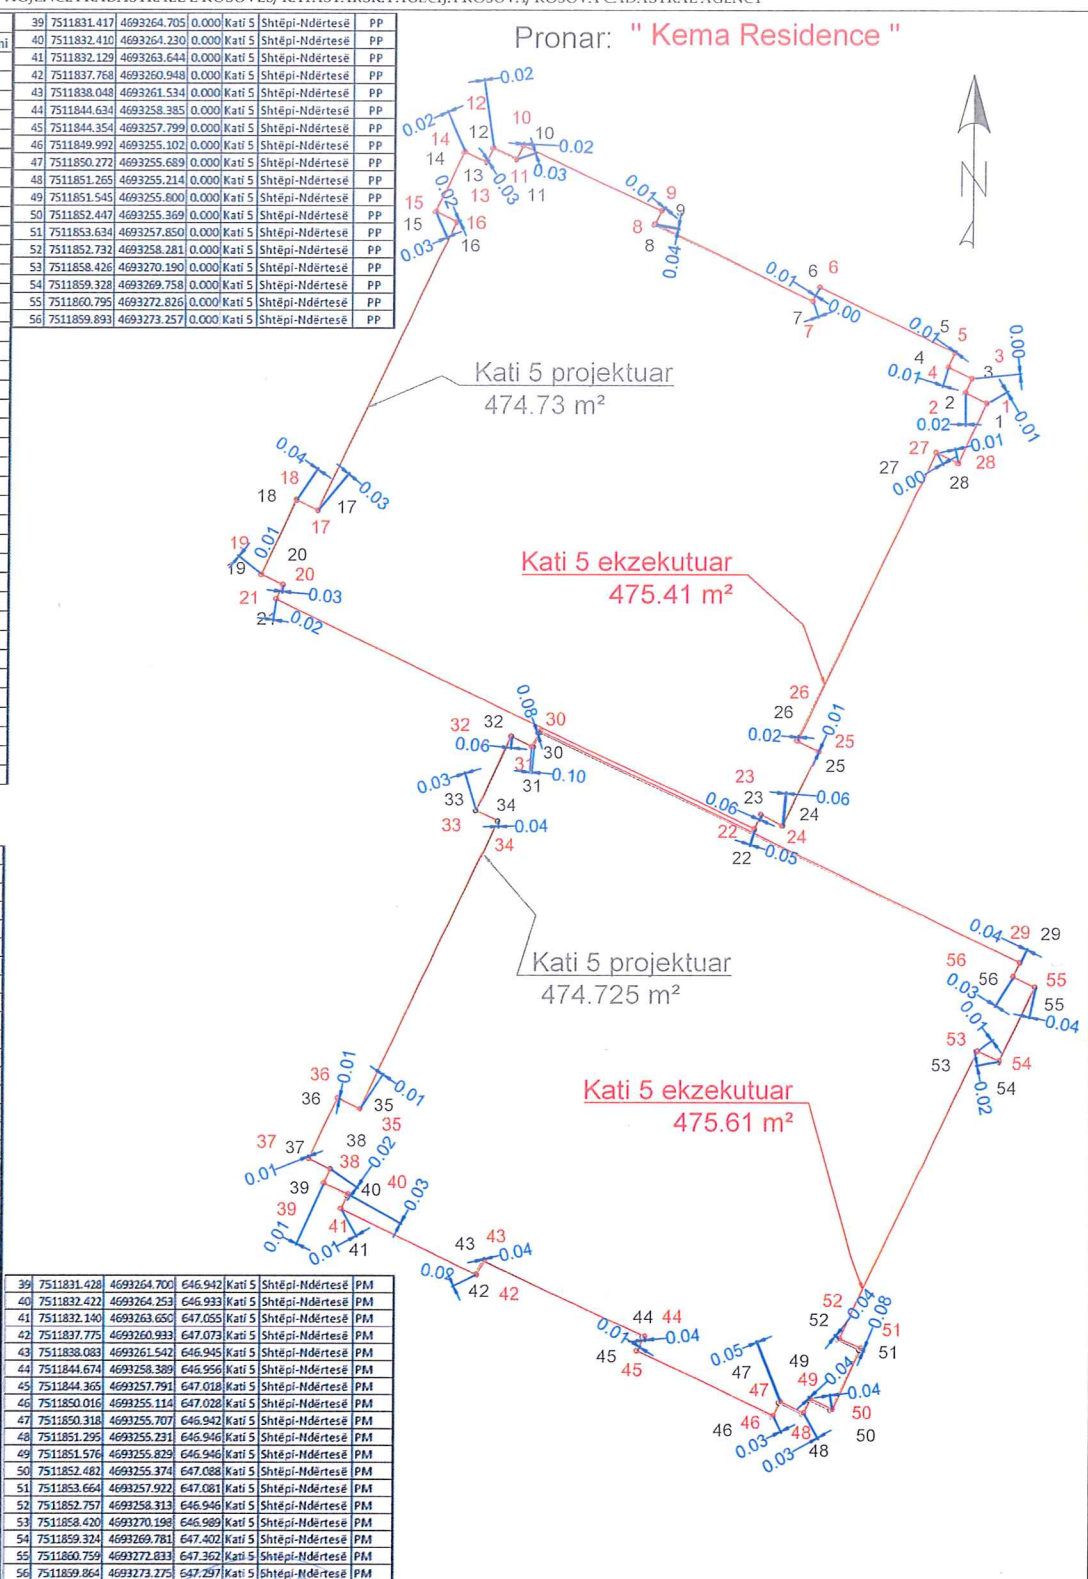

Rilevoi / Snimio: Liridon Sejdiu
(emri dhe mbiemri i gjeodetit/kompanisë/ ime i prezime geodeta/ kompanije)

Nr. i licencës / Br. licence: 140

Nënshkrimi / Potpis:

Data e rilevimit / Datum snimanja: 04/07/2026

Etazha: Kati 5

Nënshkrimi / Potpis:

Data e aprovimit / Datum usvajanja:

Zyra kadastrale komunale / Opštinska katastarska kancelarija: Ferizaj



Nr. i njësish kadastrale / Br. katastarske jedinice : 03520-0

Zona kadastrale / Katastarska zona: Ferizaj

Numri i lëndës / Broj predmeta: _____

Lloji i njësish kadastrale / Vrsta katastarske jedinice : Situacion objektit

Shkalla e zvoglimit / Razmera plana : 1:300

Republika e Kosovës
Republika Kosova-Republic of Kosova
Qeveria -Vlada-GovernmentMinistria e Mjedisit dhe Planifikimit Hapësinor /Ministarstvo Sredine i Prostornog Planiranjja/Ministry of Environment and Spatial Planning
AGJENCIA KADASTRALE E KOSOVËS/ KATASTARSKA AGENCIJA KOSOVA/ KOSOVA CADASTRAL AGENCY

Koordinatat e Kati 6 të projektuar						
Nr	Y	X	H	Kodi	Përshkrimi	Burimi
1	7511858.648	4693296.954	0.000	Kati 6	Shtëpi-Ndërtesë	PP
2	7511857.746	4693297.395	0.000	Kati 6	Shtëpi-Ndërtesë	PP
3	7511858.026	4693297.982	0.000	Kati 6	Shtëpi-Ndërtesë	PP
4	7511857.034	4693298.456	0.000	Kati 6	Shtëpi-Ndërtesë	PP
5	7511857.315	4693299.042	0.000	Kati 6	Shtëpi-Ndërtesë	PP
6	7511851.676	4693301.739	0.000	Kati 6	Shtëpi-Ndërtesë	PP
7	7511851.396	4693301.152	0.000	Kati 6	Shtëpi-Ndërtesë	PP
8	7511844.810	4693304.302	0.000	Kati 6	Shtëpi-Ndërtesë	PP
9	7511845.090	4693304.888	0.000	Kati 6	Shtëpi-Ndërtesë	PP
10	7511839.452	4693307.584	0.000	Kati 6	Shtëpi-Ndërtesë	PP
11	7511839.171	4693306.988	0.000	Kati 6	Shtëpi-Ndërtesë	PP
12	7511838.179	4693307.472	0.000	Kati 6	Shtëpi-Ndërtesë	PP
13	7511837.899	4693306.886	0.000	Kati 6	Shtëpi-Ndërtesë	PP
14	7511836.996	4693307.317	0.000	Kati 6	Shtëpi-Ndërtesë	PP
15	7511835.810	4693304.836	0.000	Kati 6	Shtëpi-Ndërtesë	PP
16	7511836.712	4693304.405	0.000	Kati 6	Shtëpi-Ndërtesë	PP
17	7511831.018	4693292.497	0.000	Kati 6	Shtëpi-Ndërtesë	PP
18	7511830.116	4693292.928	0.000	Kati 6	Shtëpi-Ndërtesë	PP
19	7511828.649	4693289.861	0.000	Kati 6	Shtëpi-Ndërtesë	PP
20	7511829.551	4693289.429	0.000	Kati 6	Shtëpi-Ndërtesë	PP
21	7511829.271	4693288.843	0.000	Kati 6	Shtëpi-Ndërtesë	PP
22	7511849.118	4693279.352	0.000	Kati 6	Shtëpi-Ndërtesë	PP
23	7511849.398	4693279.938	0.000	Kati 6	Shtëpi-Ndërtesë	PP
24	7511850.301	4693279.507	0.000	Kati 6	Shtëpi-Ndërtesë	PP
25	7511851.767	4693282.574	0.000	Kati 6	Shtëpi-Ndërtesë	PP
26	7511850.865	4693283.006	0.000	Kati 6	Shtëpi-Ndërtesë	PP
27	7511856.560	4693294.914	0.000	Kati 6	Shtëpi-Ndërtesë	PP
28	7511857.462	4693294.483	0.000	Kati 6	Shtëpi-Ndërtesë	PP
29	7511860.173	4693273.844	0.000	Kati 6	Shtëpi-Ndërtesë	PP
30	7511840.326	4693283.335	0.000	Kati 6	Shtëpi-Ndërtesë	PP
31	7511840.045	4693282.748	0.000	Kati 6	Shtëpi-Ndërtesë	PP
32	7511839.143	4693283.180	0.000	Kati 6	Shtëpi-Ndërtesë	PP
33	7511837.677	4693280.112	0.000	Kati 6	Shtëpi-Ndërtesë	PP
34	7511838.579	4693279.681	0.000	Kati 6	Shtëpi-Ndërtesë	PP
35	7511832.884	4693267.772	0.000	Kati 6	Shtëpi-Ndërtesë	PP
36	7511831.982	4693268.204	0.000	Kati 6	Shtëpi-Ndërtesë	PP
37	7511830.796	4693265.723	0.000	Kati 6	Shtëpi-Ndërtesë	PP
38	7511831.698	4693265.291	0.000	Kati 6	Shtëpi-Ndërtesë	PP

Koordinatat e Kati 6 të ekzekutuar						
Nr	Y	X	H	Kodi	Përshkrimi	Burimi
1	7511858.656	4693296.963	650.142	Kati 6	Shtëpi-Ndërtesë	PM
2	7511857.752	4693297.400	650.059	Kati 6	Shtëpi-Ndërtesë	PM
3	7511858.059	4693298.000	650.015	Kati 6	Shtëpi-Ndërtesë	PM
4	7511857.070	4693298.481	650.103	Kati 6	Shtëpi-Ndërtesë	PM
5	7511857.331	4693299.039	650.124	Kati 6	Shtëpi-Ndërtesë	PM
6	7511851.649	4693301.733	650.122	Kati 6	Shtëpi-Ndërtesë	PM
7	7511851.376	4693301.178	650.104	Kati 6	Shtëpi-Ndërtesë	PM
8	7511844.794	4693304.297	650.017	Kati 6	Shtëpi-Ndërtesë	PM
9	7511845.094	4693304.895	650.108	Kati 6	Shtëpi-Ndërtesë	PM
10	7511839.437	4693307.607	650.126	Kati 6	Shtëpi-Ndërtesë	PM
11	7511839.142	4693306.988	650.027	Kati 6	Shtëpi-Ndërtesë	PM
12	7511838.134	4693307.476	650.011	Kati 6	Shtëpi-Ndërtesë	PM
13	7511837.876	4693306.899	650.022	Kati 6	Shtëpi-Ndërtesë	PM
14	7511837.023	4693307.294	650.114	Kati 6	Shtëpi-Ndërtesë	PM
15	7511835.833	4693304.801	650.122	Kati 6	Shtëpi-Ndërtesë	PM
16	7511836.689	4693304.400	650.009	Kati 6	Shtëpi-Ndërtesë	PM
17	7511830.986	4693292.551	650.100	Kati 6	Shtëpi-Ndërtesë	PM
18	7511830.087	4693292.981	650.100	Kati 6	Shtëpi-Ndërtesë	PM
19	7511828.642	4693289.867	650.115	Kati 6	Shtëpi-Ndërtesë	PM
20	7511829.544	4693289.449	650.028	Kati 6	Shtëpi-Ndërtesë	PM
21	7511829.281	4693288.842	650.136	Kati 6	Shtëpi-Ndërtesë	PM
22	7511849.074	4693279.352	650.092	Kati 6	Shtëpi-Ndërtesë	PM
23	7511849.355	4693279.952	650.055	Kati 6	Shtëpi-Ndërtesë	PM
24	7511850.255	4693279.513	650.125	Kati 6	Shtëpi-Ndërtesë	PM
25	7511851.759	4693282.575	650.128	Kati 6	Shtëpi-Ndërtesë	PM
26	7511850.867	4693283.004	650.054	Kati 6	Shtëpi-Ndërtesë	PM
27	7511856.590	4693294.921	650.016	Kati 6	Shtëpi-Ndërtesë	PM
28	7511857.470	4693294.461	650.144	Kati 6	Shtëpi-Ndërtesë	PM
29	7511860.176	4693273.845	650.000	Kati 6	Shtëpi-Ndërtesë	PM
30	7511840.283	4693283.347	649.996	Kati 6	Shtëpi-Ndërtesë	PM
31	7511840.001	4693282.738	650.012	Kati 6	Shtëpi-Ndërtesë	PM
32	7511839.105	4693283.187	650.150	Kati 6	Shtëpi-Ndërtesë	PM
33	7511837.627	4693280.107	650.107	Kati 6	Shtëpi-Ndërtesë	PM
34	7511838.502	4693279.674	650.105	Kati 6	Shtëpi-Ndërtesë	PM
35	7511832.906	4693267.743	650.004	Kati 6	Shtëpi-Ndërtesë	PM
36	7511831.996	4693268.180	650.137	Kati 6	Shtëpi-Ndërtesë	PM
37	7511830.796	4693265.691	650.122	Kati 6	Shtëpi-Ndërtesë	PM
38	7511831.705	4693265.248	650.009	Kati 6	Shtëpi-Ndërtesë	PM

39	7511831.417	4693264.705	0.000	Kati 6	Shtëpi-Ndërtesë	PP
40	7511832.410	4693264.230	0.000	Kati 6	Shtëpi-Ndërtesë	PP
41	7511832.129	4693263.644	0.000	Kati 6	Shtëpi-Ndërtesë	PP
42	7511837.768	4693260.948	0.000	Kati 6	Shtëpi-Ndërtesë	PP
43	7511838.048	4693261.534	0.000	Kati 6	Shtëpi-Ndërtesë	PP
44	7511844.634	4693258.385	0.000	Kati 6	Shtëpi-Ndërtesë	PP
45	7511844.354	4693257.799	0.000	Kati 6	Shtëpi-Ndërtesë	PP
46	7511849.992	4693255.102	0.000	Kati 6	Shtëpi-Ndërtesë	PP
47	7511850.272	4693255.689	0.000	Kati 6	Shtëpi-Ndërtesë	PP
48	7511851.265	4693255.214	0.000	Kati 6	Shtëpi-Ndërtesë	PP
49	7511851.545	4693255.800	0.000	Kati 6	Shtëpi-Ndërtesë	PP
50	7511852.447	4693255.369	0.000	Kati 6	Shtëpi-Ndërtesë	PP
51	7511853.634	4693257.850	0.000	Kati 6	Shtëpi-Ndërtesë	PP
52	7511852.732	4693258.281	0.000	Kati 6	Shtëpi-Ndërtesë	PP
53	7511858.426	4693270.190	0.000	Kati 6	Shtëpi-Ndërtesë	PP
54	7511859.328	4693269.758	0.000	Kati 6	Shtëpi-Ndërtesë	PP
55	7511860.795	4693272.826	0.000	Kati 6	Shtëpi-Ndërtesë	PP
56	7511859.893	4693273.257	0.000	Kati 6	Shtëpi-Ndërtesë	PP

39	7511831.420	4693264.679	649.993	Kati 6	Shtëpi-Ndërtesë	PM
40	7511832.399	4693264.201	650.137	Kati 6	Shtëpi-Ndërtesë	PM
41	7511832.141	4693263.627	650.105	Kati 6	Shtëpi-Ndërtesë	PM
42	7511837.780	4693260.980	650.111	Kati 6	Shtëpi-Ndërtesë	PM
43	7511838.068	4693261.511	650.010	Kati 6	Shtëpi-Ndërtesë	PM
44	7511844.607	4693258.360	650.141	Kati 6	Shtëpi-Ndërtesë	PM
45	7511844.339	4693257.781	650.126	Kati 6	Shtëpi-Ndërtesë	PM
46	7511849.992	4693255.089	650.136	Kati 6	Shtëpi-Ndërtesë	PM
47	7511850.272	4693255.641	650.146	Kati 6	Shtëpi-Ndërtesë	PM
48	7511851.257	4693255.209	650.014	Kati 6	Shtëpi-Ndërtesë	PM
49	7511851.536	4693255.801	650.018	Kati 6	Shtëpi-Ndërtesë	PM
50	7511852.442	4693255.356	650.110	Kati 6	Shtëpi-Ndërtesë	PM
51	7511853.641	4693257.861	650.119	Kati 6	Shtëpi-Ndërtesë	PM
52	7511852.737	4693258.290	650.020	Kati 6	Shtëpi-Ndërtesë	PM
53	7511858.438	4693270.196	650.030	Kati 6	Shtëpi-Ndërtesë	PM
54	7511859.319	4693269.740	650.106	Kati 6	Shtëpi-Ndërtesë	PM
55	7511860.787	4693272.826	650.093	Kati 6	Shtëpi-Ndërtesë	PM
56	7511859.897	4693273.256	650.002	Kati 6	Shtëpi-Ndërtesë	PM

Pronar: " Kema Residence "

Kati 6 projektuar
474.73 m²Kati 6 ekzekutuar
475.64 m²Kati 6 projektuar
474.73 m²Kati 6 ekzekutuar
475.52 m²Rilevoi / Snimio: Liridon Sejdiu
(emri dhe mbiemri i gjeodetit/kompanisë/ ime i prezime gjeodeti/ kompanije)

Nr. i licencës / Br. licence: 140

Nënshkrimi / Potpis:

Data e rilevimit / Datum snimanja: 18/07/2026

Etazha: Kati 6

Nënshkrimi / Potpis:

Data e aprovimit / Datum usvajanja:

Zyra kadastrale komunale / Opštinska katastarska kancelarija: Ferizaj

Zona kadastrale / Katastarska zona: Ferizaj

Lloji i njësish kadastrale / Vrsta katastarske jedinice : Situacion objektit



Nr. i njësish kadastrale / Br. katastarske jedinice : 03520-0

Numri i lëndës / Broj predmeta:

Shkalla e zvoglimit / Razmera plana : 1:300

Republika e Kosovës
Republika Kosova-Republic of Kosova
Qeveria -Vlada-Government

Ministria e Mjedisit dhe Planifikimit Hapësinor / Ministarstvo Sredine i Prostornog Planiranja/Ministry of Environment and Spatial Planning
AGJENCIA KADASTRALE E KOSOVËS/ KATASTARSKA AGENCIJA KOSOVA/ KOSOVA CADASTRAL AGENCY


Koordinatat e Kati 7 të projektuar						
Nr	Y	X	H	Kodi	Përshkrimi	Burimi
1	7511858.648	4693296.964	0.000	Kati 7	Shtëpi-Ndërtesë	PP
2	7511857.746	4693297.395	0.000	Kati 7	Shtëpi-Ndërtesë	PP
3	7511858.026	4693297.982	0.000	Kati 7	Shtëpi-Ndërtesë	PP
4	7511857.034	4693298.456	0.000	Kati 7	Shtëpi-Ndërtesë	PP
5	7511857.315	4693299.042	0.000	Kati 7	Shtëpi-Ndërtesë	PP
6	7511851.676	4693301.739	0.000	Kati 7	Shtëpi-Ndërtesë	PP
7	7511851.396	4693301.152	0.000	Kati 7	Shtëpi-Ndërtesë	PP
8	7511844.810	4693304.302	0.000	Kati 7	Shtëpi-Ndërtesë	PP
9	7511845.090	4693304.888	0.000	Kati 7	Shtëpi-Ndërtesë	PP
10	7511839.452	4693307.584	0.000	Kati 7	Shtëpi-Ndërtesë	PP
11	7511839.171	4693306.998	0.000	Kati 7	Shtëpi-Ndërtesë	PP
12	7511838.179	4693307.472	0.000	Kati 7	Shtëpi-Ndërtesë	PP
13	7511837.899	4693306.886	0.000	Kati 7	Shtëpi-Ndërtesë	PP
14	7511836.996	4693307.317	0.000	Kati 7	Shtëpi-Ndërtesë	PP
15	7511835.810	4693304.836	0.000	Kati 7	Shtëpi-Ndërtesë	PP
16	7511836.712	4693304.405	0.000	Kati 7	Shtëpi-Ndërtesë	PP
17	7511831.018	4693292.497	0.000	Kati 7	Shtëpi-Ndërtesë	PP
18	7511830.116	4693292.928	0.000	Kati 7	Shtëpi-Ndërtesë	PP
19	7511828.649	4693289.861	0.000	Kati 7	Shtëpi-Ndërtesë	PP
20	7511829.551	4693289.429	0.000	Kati 7	Shtëpi-Ndërtesë	PP
21	7511829.271	4693288.843	0.000	Kati 7	Shtëpi-Ndërtesë	PP
22	7511849.118	4693279.352	0.000	Kati 7	Shtëpi-Ndërtesë	PP
23	7511849.398	4693279.938	0.000	Kati 7	Shtëpi-Ndërtesë	PP
24	7511850.301	4693279.507	0.000	Kati 7	Shtëpi-Ndërtesë	PP
25	7511851.767	4693282.574	0.000	Kati 7	Shtëpi-Ndërtesë	PP
26	7511850.865	4693283.006	0.000	Kati 7	Shtëpi-Ndërtesë	PP
27	7511856.560	4693294.914	0.000	Kati 7	Shtëpi-Ndërtesë	PP
28	7511857.462	4693294.483	0.000	Kati 7	Shtëpi-Ndërtesë	PP
29	7511860.173	4693273.844	0.000	Kati 7	Shtëpi-Ndërtesë	PP
30	7511840.326	4693283.335	0.000	Kati 7	Shtëpi-Ndërtesë	PP
31	7511840.045	4693282.748	0.000	Kati 7	Shtëpi-Ndërtesë	PP
32	7511839.143	4693283.180	0.000	Kati 7	Shtëpi-Ndërtesë	PP
33	7511837.677	4693280.112	0.000	Kati 7	Shtëpi-Ndërtesë	PP
34	7511838.579	4693279.681	0.000	Kati 7	Shtëpi-Ndërtesë	PP
35	7511832.884	4693267.772	0.000	Kati 7	Shtëpi-Ndërtesë	PP
36	7511831.982	4693268.204	0.000	Kati 7	Shtëpi-Ndërtesë	PP
37	7511830.796	4693265.723	0.000	Kati 7	Shtëpi-Ndërtesë	PP
38	7511831.698	4693265.291	0.000	Kati 7	Shtëpi-Ndërtesë	PP

Koordinatat e Kati 7 të ekzekutuar						
Nr	Y	X	H	Kodi	Përshkrimi	Burimi
1	7511858.666	4693296.968	653.151	Kati 7	Shtëpi-Ndërtesë	PM
2	7511857.781	4693297.396	653.054	Kati 7	Shtëpi-Ndërtesë	PM
3	7511858.032	4693297.977	653.049	Kati 7	Shtëpi-Ndërtesë	PM
4	7511857.076	4693298.504	653.142	Kati 7	Shtëpi-Ndërtesë	PM
5	7511857.345	4693299.051	653.124	Kati 7	Shtëpi-Ndërtesë	PM
6	7511851.670	4693301.727	653.143	Kati 7	Shtëpi-Ndërtesë	PM
7	7511851.398	4693301.184	653.128	Kati 7	Shtëpi-Ndërtesë	PM
8	7511844.805	4693304.310	653.164	Kati 7	Shtëpi-Ndërtesë	PM
9	7511845.068	4693304.859	653.119	Kati 7	Shtëpi-Ndërtesë	PM
10	7511839.439	4693307.578	653.145	Kati 7	Shtëpi-Ndërtesë	PM
11	7511839.176	4693307.026	653.142	Kati 7	Shtëpi-Ndërtesë	PM
12	7511838.185	4693307.477	653.042	Kati 7	Shtëpi-Ndërtesë	PM
13	7511837.875	4693306.924	653.141	Kati 7	Shtëpi-Ndërtesë	PM
14	7511837.051	4693307.312	653.135	Kati 7	Shtëpi-Ndërtesë	PM
15	7511835.848	4693304.804	653.189	Kati 7	Shtëpi-Ndërtesë	PM
16	7511836.673	4693304.411	653.151	Kati 7	Shtëpi-Ndërtesë	PM
17	7511831.050	4693292.498	653.044	Kati 7	Shtëpi-Ndërtesë	PM
18	7511830.136	4693292.926	653.146	Kati 7	Shtëpi-Ndërtesë	PM
19	7511828.659	4693289.880	653.154	Kati 7	Shtëpi-Ndërtesë	PM
20	7511829.531	4693289.442	653.130	Kati 7	Shtëpi-Ndërtesë	PM
21	7511829.256	4693288.844	653.071	Kati 7	Shtëpi-Ndërtesë	PM
22	7511849.092	4693279.355	653.027	Kati 7	Shtëpi-Ndërtesë	PM
23	7511849.400	4693279.924	653.145	Kati 7	Shtëpi-Ndërtesë	PM
24	7511850.267	4693279.508	653.144	Kati 7	Shtëpi-Ndërtesë	PM
25	7511851.755	4693282.573	653.140	Kati 7	Shtëpi-Ndërtesë	PM
26	7511850.867	4693283.000	653.137	Kati 7	Shtëpi-Ndërtesë	PM
27	7511856.592	4693294.906	653.367	Kati 7	Shtëpi-Ndërtesë	PM
28	7511857.485	4693294.501	653.154	Kati 7	Shtëpi-Ndërtesë	PM
29	7511860.173	4693273.849	653.043	Kati 7	Shtëpi-Ndërtesë	PM
30	7511840.357	4693283.340	653.052	Kati 7	Shtëpi-Ndërtesë	PM
31	7511840.027	4693282.758	653.168	Kati 7	Shtëpi-Ndërtesë	PM
32	7511839.158	4693283.186	653.162	Kati 7	Shtëpi-Ndërtesë	PM
33	7511837.671	4693280.085	653.160	Kati 7	Shtëpi-Ndërtesë	PM
34	7511838.602	4693279.653	653.061	Kati 7	Shtëpi-Ndërtesë	PM
35	7511832.902	4693267.774	653.049	Kati 7	Shtëpi-Ndërtesë	PM
36	7511831.994	4693268.216	653.143	Kati 7	Shtëpi-Ndërtesë	PM
37	7511830.797	4693265.720	653.144	Kati 7	Shtëpi-Ndërtesë	PM
38	7511831.709	4693265.288	653.052	Kati 7	Shtëpi-Ndërtesë	PM

39	7511831.417	4693264.705	0.000	Kati 7	Shtëpi-Ndërtesë	PP
40	7511832.410	4693264.230	0.000	Kati 7	Shtëpi-Ndërtesë	PP
41	7511832.129	4693263.644	0.000	Kati 7	Shtëpi-Ndërtesë	PP
42	7511837.768	4693260.948	0.000	Kati 7	Shtëpi-Ndërtesë	PP
43	7511838.048	4693261.534	0.000	Kati 7	Shtëpi-Ndërtesë	PP
44	7511844.634	4693258.385	0.000	Kati 7	Shtëpi-Ndërtesë	PP
45	7511844.354	4693257.799	0.000	Kati 7	Shtëpi-Ndërtesë	PP
46	7511849.992	4693255.102	0.000	Kati 7	Shtëpi-Ndërtesë	PP
47	7511850.272	4693255.689	0.000	Kati 7	Shtëpi-Ndërtesë	PP
48	7511851.265	4693255.214	0.000	Kati 7	Shtëpi-Ndërtesë	PP
49	7511851.545	4693255.800	0.000	Kati 7	Shtëpi-Ndërtesë	PP
50	7511852.447	4693255.369	0.000	Kati 7	Shtëpi-Ndërtesë	PP
51	7511853.634	4693257.850	0.000	Kati 7	Shtëpi-Ndërtesë	PP
52	7511852.732	4693258.281	0.000	Kati 7	Shtëpi-Ndërtesë	PP
53	7511858.426	4693270.190	0.000	Kati 7	Shtëpi-Ndërtesë	PP
54	7511859.328	4693269.758	0.000	Kati 7	Shtëpi-Ndërtesë	PP
55	7511860.795	4693272.826	0.000	Kati 7	Shtëpi-Ndërtesë	PP
56	7511859.893	4693273.257	0.000	Kati 7	Shtëpi-Ndërtesë	PP

39	7511831.421	4693264.707	653.043	Kati 7	Shtëpi-Ndërtesë	PM
40	7511832.402	4693264.218	653.178	Kati 7	Shtëpi-Ndërtesë	PM
41	7511832.132	4693263.649	653.142	Kati 7	Shtëpi-Ndërtesë	PM
42	7511837.776	4693260.936	653.155	Kati 7	Shtëpi-Ndërtesë	PM
43	7511838.069	4693261.522	653.047	Kati 7	Shtëpi-Ndërtesë	PM
44	7511844.592	4693258.359	653.165	Kati 7	Shtëpi-Ndërtesë	PM
45	7511844.330	4693257.795	653.172	Kati 7	Shtëpi-Ndërtesë	PM
46	7511849.982	4693255.096	653.152	Kati 7	Shtëpi-Ndërtesë	PM
47	7511850.256	4693255.637	653.149	Kati 7	Shtëpi-Ndërtesë	PM
48	7511851.248	4693255.212	653.058	Kati 7	Shtëpi-Ndërtesë	PM
49	7511851.543	4693255.781	653.066	Kati 7	Shtëpi-Ndërtesë	PM
50	7511852.441	4693255.351	653.155	Kati 7	Shtëpi-Ndërtesë	PM
51	7511853.625	4693257.855	653.182	Kati 7	Shtëpi-Ndërtesë	PM
52	7511852.748	4693258.277	653.150	Kati 7	Shtëpi-Ndërtesë	PM
53	7511858.402	4693270.184	653.059	Kati 7	Shtëpi-Ndërtesë	PM
54	7511859.324	4693269.744	653.152	Kati 7	Shtëpi-Ndërtesë	PM
55	7511860.778	4693272.828	653.137	Kati 7	Shtëpi-Ndërtesë	PM
56	7511859.886	4693273.253	653.057	Kati 7	Shtëpi-Ndërtesë	PM

Pronar: " Kema Residence "

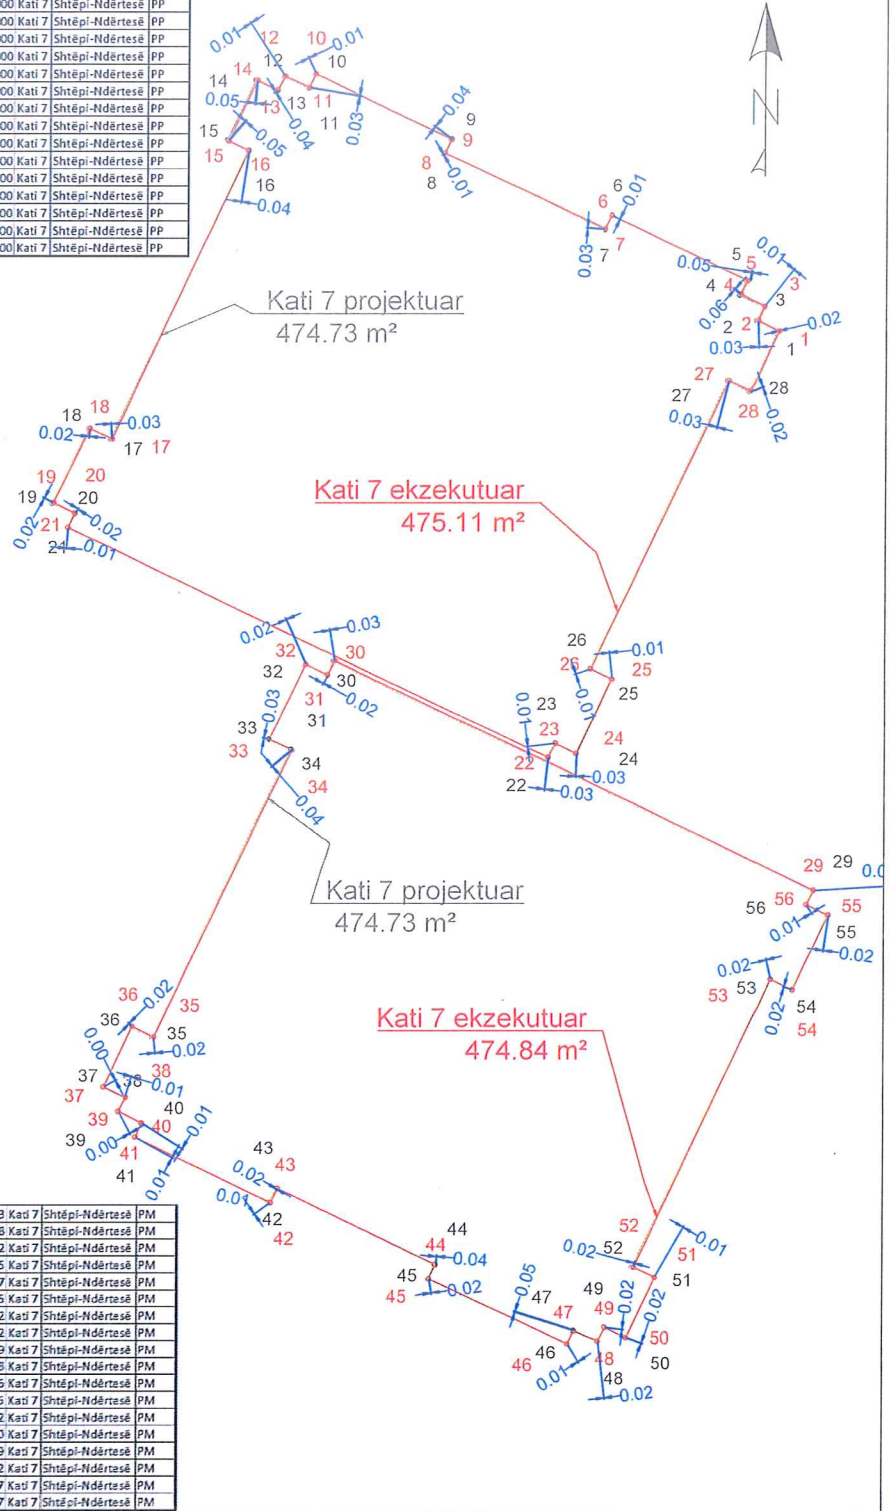

Rilevoi / Snimio: Liridon Sejdiu
(emri dhe mbiemri i gjeodetit/kompanisë/ ime i prezime geodeta/ kompanije)

Nr. i licencës / Br. licence: 140

Nënshkrimi / Potpis:

Data e rilevimit / Datum snimanja: 31/07/2026

Etazha: Kati 7

Nënshkrimi / Potpis:

Data e aprovimit / Datum usvajanja:

