

Zyra kadastrale komunale / Opštinska katastarska kancelarija: Ferizaj

Zona kadastrale / Katastarska zona: Ferizaj

Lloji i njësisë kadastrale / Vrstë katastarske jedinice : Situacion objektit



Nr. i njësisë kadastrale / Br. katastarske jedinice : 03520-0

Numri i lëndës / Broj predmeta:

Shkalla e zvoglimit / Razmera plana : 1:300

Republika e Kosovës
Republika Kosova-Republic of Kosovo
Qeveria -Vlada-Government


Ministria e Mjedisit dhe Planifikimit Hapësinor /Ministarstvo Sredine i Prostornog Planiranja/Ministry of Environment and Spatial Planning

AGJENCIA KADASTRALE E KOSOVËS/ KATASTARSKA AGENCIJA KOSOVA/ KOSOVA CADASTRAL AGENCY

Koordinatat e Kati 8 të projektuar					
Nr	Y	X	H	Kodi	Përshkrimi
1	7511858.648	4693296.964	0.000	Kati 8	Shtëpi-Ndërtesë PP
2	7511857.746	4693297.395	0.000	Kati 8	Shtëpi-Ndërtesë PP
3	7511858.026	4693297.982	0.000	Kati 8	Shtëpi-Ndërtesë PP
4	7511857.034	4693298.456	0.000	Kati 8	Shtëpi-Ndërtesë PP
5	7511857.315	4693299.042	0.000	Kati 8	Shtëpi-Ndërtesë PP
6	7511851.676	4693301.739	0.000	Kati 8	Shtëpi-Ndërtesë PP
7	7511851.396	4693301.152	0.000	Kati 8	Shtëpi-Ndërtesë PP
8	7511844.810	4693304.302	0.000	Kati 8	Shtëpi-Ndërtesë PP
9	7511845.090	4693304.888	0.000	Kati 8	Shtëpi-Ndërtesë PP
10	7511839.452	4693307.584	0.000	Kati 8	Shtëpi-Ndërtesë PP
11	7511839.171	4693306.998	0.000	Kati 8	Shtëpi-Ndërtesë PP
12	7511838.179	4693307.472	0.000	Kati 8	Shtëpi-Ndërtesë PP
13	7511837.899	4693306.886	0.000	Kati 8	Shtëpi-Ndërtesë PP
14	7511836.996	4693307.317	0.000	Kati 8	Shtëpi-Ndërtesë PP
15	7511835.810	4693304.836	0.000	Kati 8	Shtëpi-Ndërtesë PP
16	7511836.712	4693304.405	0.000	Kati 8	Shtëpi-Ndërtesë PP
17	7511831.018	4693292.497	0.000	Kati 8	Shtëpi-Ndërtesë PP
18	7511830.116	4693292.928	0.000	Kati 8	Shtëpi-Ndërtesë PP
19	7511828.649	4693289.861	0.000	Kati 8	Shtëpi-Ndërtesë PP
20	7511829.551	4693289.429	0.000	Kati 8	Shtëpi-Ndërtesë PP
21	7511829.271	4693288.843	0.000	Kati 8	Shtëpi-Ndërtesë PP
22	7511849.118	4693279.352	0.000	Kati 8	Shtëpi-Ndërtesë PP
23	7511849.398	4693279.938	0.000	Kati 8	Shtëpi-Ndërtesë PP
24	7511850.301	4693279.507	0.000	Kati 8	Shtëpi-Ndërtesë PP
25	7511851.767	4693282.574	0.000	Kati 8	Shtëpi-Ndërtesë PP
26	7511850.865	4693283.006	0.000	Kati 8	Shtëpi-Ndërtesë PP
27	7511856.560	4693294.914	0.000	Kati 8	Shtëpi-Ndërtesë PP
28	7511857.462	4693294.483	0.000	Kati 8	Shtëpi-Ndërtesë PP
29	7511860.173	4693273.844	0.000	Kati 8	Shtëpi-Ndërtesë PP
30	7511840.326	4693283.335	0.000	Kati 8	Shtëpi-Ndërtesë PP
31	7511840.045	4693282.748	0.000	Kati 8	Shtëpi-Ndërtesë PP
32	7511839.143	4693283.180	0.000	Kati 8	Shtëpi-Ndërtesë PP
33	7511837.677	4693280.112	0.000	Kati 8	Shtëpi-Ndërtesë PP
34	7511838.579	4693279.681	0.000	Kati 8	Shtëpi-Ndërtesë PP
35	7511832.884	4693267.772	0.000	Kati 8	Shtëpi-Ndërtesë PP
36	7511831.982	4693268.204	0.000	Kati 8	Shtëpi-Ndërtesë PP
37	7511830.796	4693265.723	0.000	Kati 8	Shtëpi-Ndërtesë PP
38	7511831.698	4693265.291	0.000	Kati 8	Shtëpi-Ndërtesë PP

Koordinatat e Kati 8 të ekzekutuar					
Nr	Y	X	H	Kodi	Përshkrimi
1	7511859.000	4693297.000	656.287	Kati 8	Shtëpi-Ndërtesë PM
2	7511858.000	4693297.000	656.287	Kati 8	Shtëpi-Ndërtesë PM
3	7511858.000	4693298.000	656.287	Kati 8	Shtëpi-Ndërtesë PM
4	7511857.000	4693299.000	656.287	Kati 8	Shtëpi-Ndërtesë PM
5	7511857.000	4693299.000	656.287	Kati 8	Shtëpi-Ndërtesë PM
6	7511852.000	4693302.000	656.287	Kati 8	Shtëpi-Ndërtesë PM
7	7511851.000	4693301.000	656.287	Kati 8	Shtëpi-Ndërtesë PM
8	7511845.000	4693304.000	656.287	Kati 8	Shtëpi-Ndërtesë PM
9	7511845.000	4693305.000	656.287	Kati 8	Shtëpi-Ndërtesë PM
10	7511839.000	4693308.000	656.287	Kati 8	Shtëpi-Ndërtesë PM
11	7511839.000	4693307.000	656.287	Kati 8	Shtëpi-Ndërtesë PM
12	7511838.000	4693307.000	656.287	Kati 8	Shtëpi-Ndërtesë PM
13	7511838.000	4693307.000	656.287	Kati 8	Shtëpi-Ndërtesë PM
14	7511837.000	4693307.000	656.287	Kati 8	Shtëpi-Ndërtesë PM
15	7511836.000	4693305.000	656.287	Kati 8	Shtëpi-Ndërtesë PM
16	7511837.000	4693304.000	656.287	Kati 8	Shtëpi-Ndërtesë PM
17	7511831.000	4693292.000	656.287	Kati 8	Shtëpi-Ndërtesë PM
18	7511830.000	4693293.000	656.287	Kati 8	Shtëpi-Ndërtesë PM
19	7511829.000	4693290.000	656.287	Kati 8	Shtëpi-Ndërtesë PM
20	7511830.000	4693289.000	656.287	Kati 8	Shtëpi-Ndërtesë PM
21	7511829.000	4693289.000	656.287	Kati 8	Shtëpi-Ndërtesë PM
22	7511849.000	4693279.000	656.287	Kati 8	Shtëpi-Ndërtesë PM
23	7511849.000	4693280.000	656.287	Kati 8	Shtëpi-Ndërtesë PM
24	7511850.000	4693280.000	656.287	Kati 8	Shtëpi-Ndërtesë PM
25	7511852.000	4693283.000	656.287	Kati 8	Shtëpi-Ndërtesë PM
26	7511851.000	4693283.000	656.287	Kati 8	Shtëpi-Ndërtesë PM
27	7511857.000	4693295.000	656.287	Kati 8	Shtëpi-Ndërtesë PM
28	7511857.000	4693295.000	656.287	Kati 8	Shtëpi-Ndërtesë PM
29	7511860.000	4693274.000	656.287	Kati 8	Shtëpi-Ndërtesë PM
30	7511840.000	4693283.000	656.287	Kati 8	Shtëpi-Ndërtesë PM
31	7511840.000	4693283.000	656.287	Kati 8	Shtëpi-Ndërtesë PM
32	7511839.000	4693283.000	656.287	Kati 8	Shtëpi-Ndërtesë PM
33	7511838.000	4693280.000	656.287	Kati 8	Shtëpi-Ndërtesë PM
34	7511839.000	4693280.000	656.287	Kati 8	Shtëpi-Ndërtesë PM
35	7511833.000	4693268.000	656.287	Kati 8	Shtëpi-Ndërtesë PM
36	7511832.000	4693268.000	656.287	Kati 8	Shtëpi-Ndërtesë PM
37	7511831.000	4693266.000	656.287	Kati 8	Shtëpi-Ndërtesë PM
38	7511832.000	4693265.000	656.287	Kati 8	Shtëpi-Ndërtesë PM

39	7511831.417	4693264.705	0.000	Kati 8	Shtëpi-Ndërtesë PP
40	7511832.410	4693264.230	0.000	Kati 8	Shtëpi-Ndërtesë PP
41	7511832.129	4693263.644	0.000	Kati 8	Shtëpi-Ndërtesë PP
42	7511837.768	4693260.948	0.000	Kati 8	Shtëpi-Ndërtesë PP
43	7511838.048	4693261.534	0.000	Kati 8	Shtëpi-Ndërtesë PP
44	7511844.634	4693258.385	0.000	Kati 8	Shtëpi-Ndërtesë PP
45	7511844.354	4693257.799	0.000	Kati 8	Shtëpi-Ndërtesë PP
46	7511849.992	4693255.102	0.000	Kati 8	Shtëpi-Ndërtesë PP
47	7511850.272	4693255.689	0.000	Kati 8	Shtëpi-Ndërtesë PP
48	7511851.265	4693255.214	0.000	Kati 8	Shtëpi-Ndërtesë PP
49	7511851.545	4693255.800	0.000	Kati 8	Shtëpi-Ndërtesë PP
50	7511852.447	4693255.369	0.000	Kati 8	Shtëpi-Ndërtesë PP
51	7511853.634	4693257.850	0.000	Kati 8	Shtëpi-Ndërtesë PP
52	7511852.732	4693258.281	0.000	Kati 8	Shtëpi-Ndërtesë PP
53	7511858.426	4693270.190	0.000	Kati 8	Shtëpi-Ndërtesë PP
54	7511859.328	4693269.758	0.000	Kati 8	Shtëpi-Ndërtesë PP
55	7511860.795	4693272.826	0.000	Kati 8	Shtëpi-Ndërtesë PP
56	7511859.893	4693273.257	0.000	Kati 8	Shtëpi-Ndërtesë PP

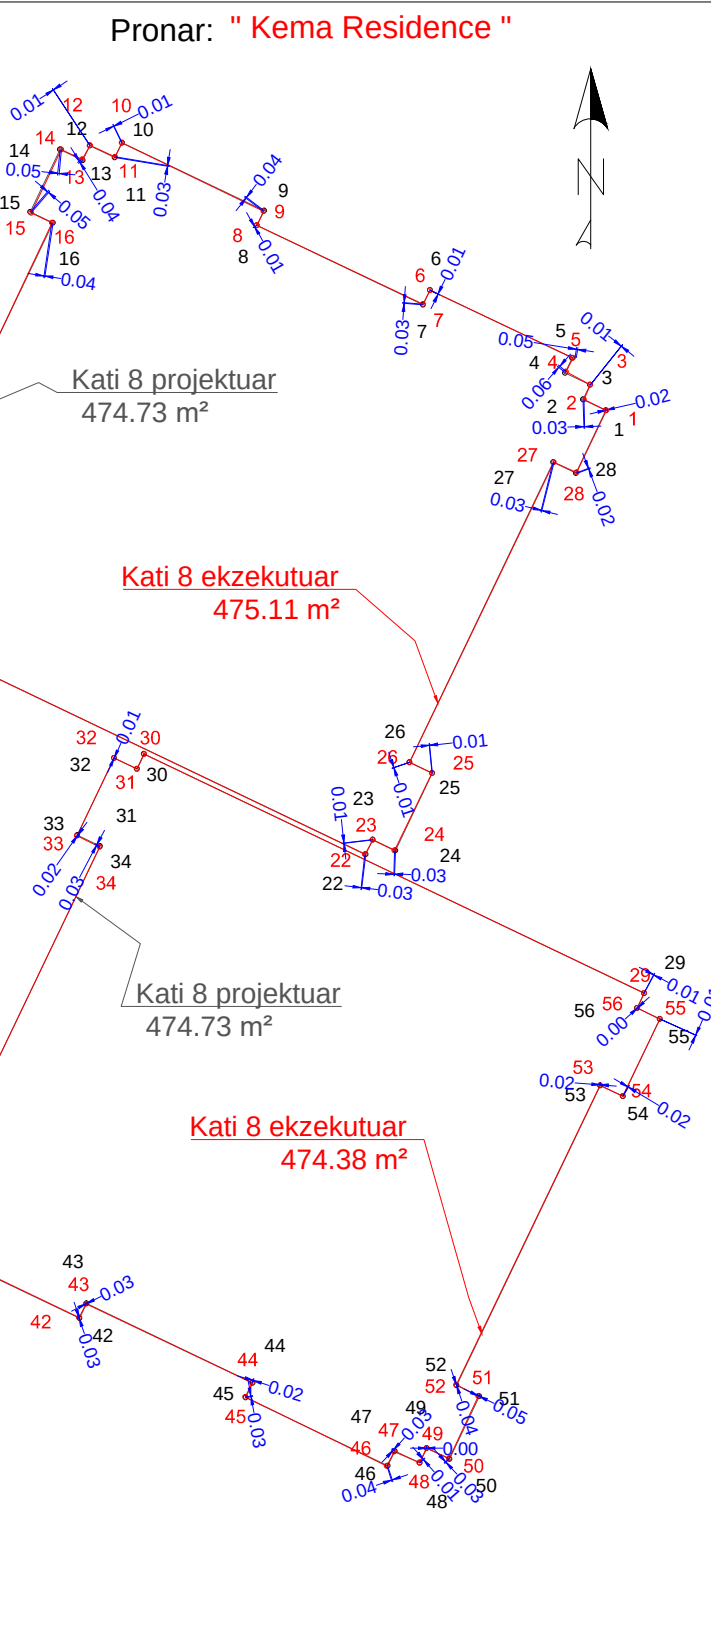

Rilevoi / Snimio: Liridon Sejdiu
(emri dhe mbiemri i gjeodetit/kompanisë/ ime i prezime geodeta/ kompanije)

Nr. i licencës / Br. licence: 140

Nënshkrimi / Potpis:

Data e rilevimit / Datum snimanja: 03/09/2026

Etazha: Kati 8

Nënshkrimi / Potpis:

Data e aprovimit / Datum usvajanja: